

NOTE:-MATERIAL FINISH HDG

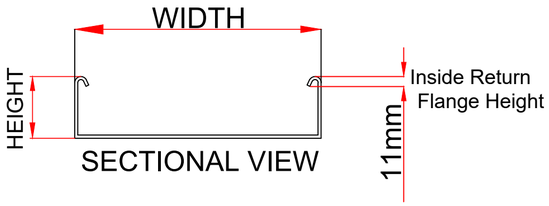

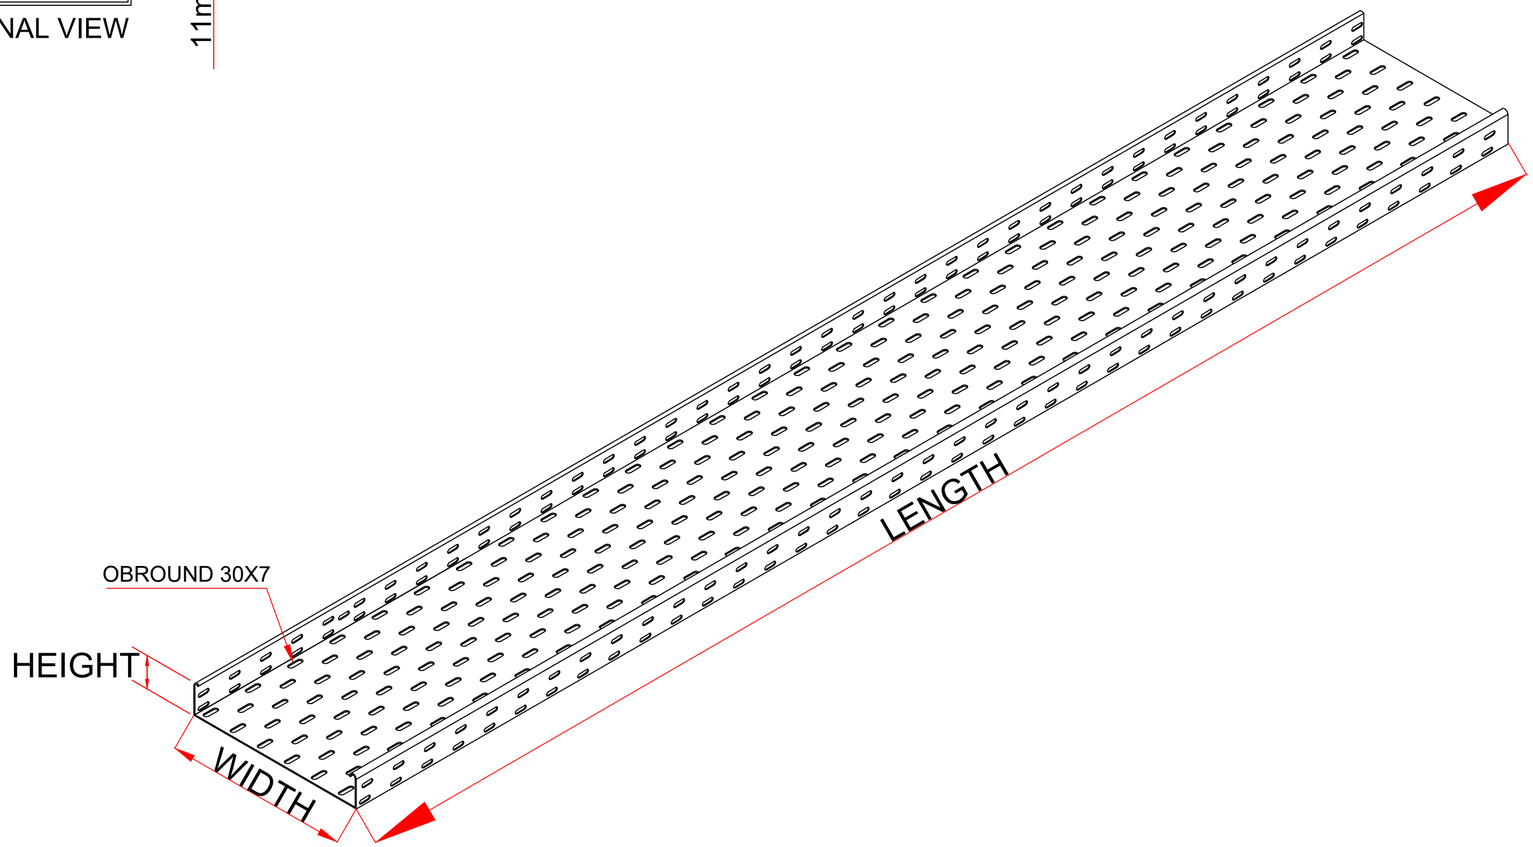

CABLE TRAY STRAIGHT

SN	DIMENSION TABLE	QTY
01	W=150mm, H=50mm, T=1.5mm & L=3000mm	67
02	W=225mm, H=50mm, T=1.5mm & L=3000mm	84
03	W=300mm, H=50mm, T=1.5mm & L=3000mm	119

DRAWN BY	SHAH ALAM	
CHECKED BY	AMIR KHAN	
APPROVED BY	NASSER ANANI	
DATE	04/05/2026	
REF NO. :		
CONSULTANT :		

TITLE: CABLE TRAY STRAIGHT

CLIENT: SITE TECHNOLOGY INTEGRATED SYSTEM LLC

SEC ITEM NO:

BONN METAL CONS. IND.

BONN GROUP OF COMPANIES
Cable Management Systems


DWRG. NO. :


SHEET NO. :

SCALE: NTS

REV. 01

NOTE:-MATERIAL FINISH HDG

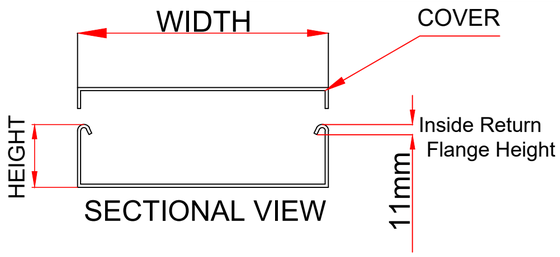

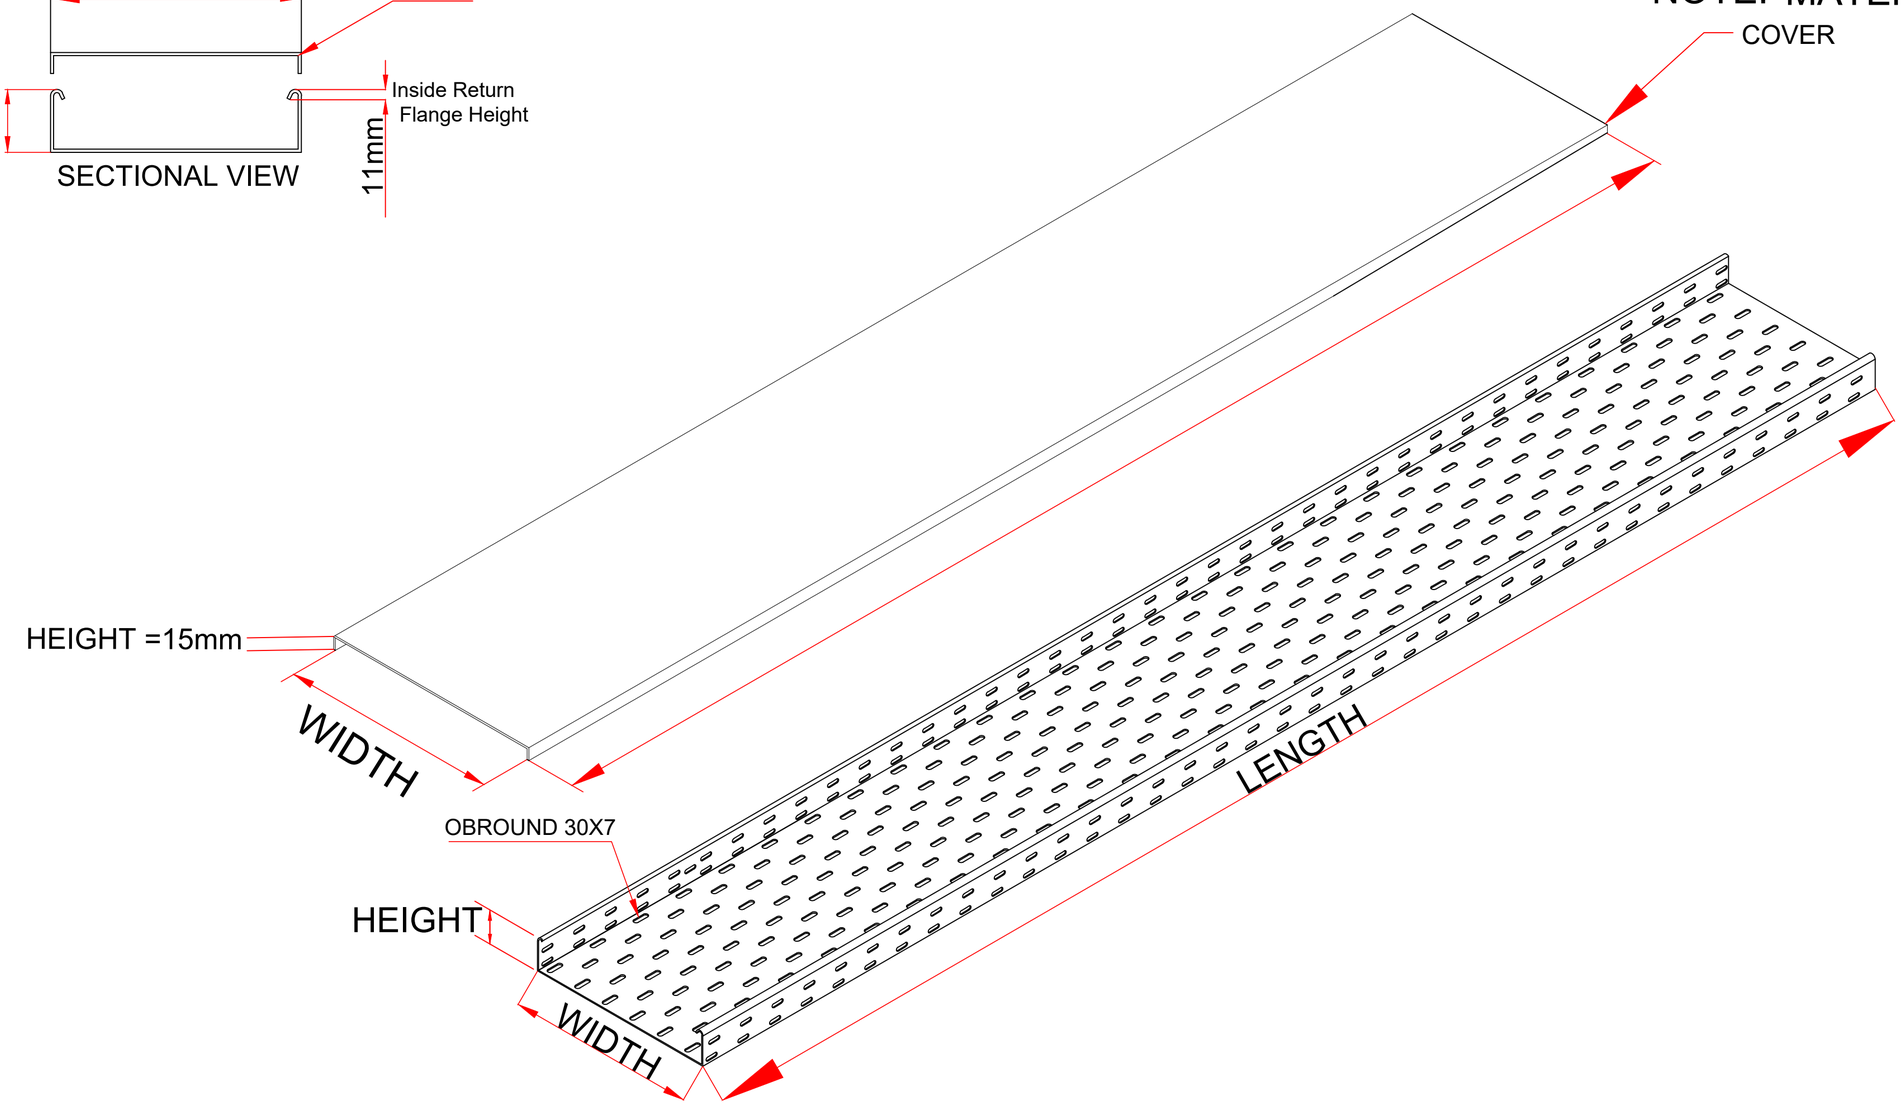

CABLE TRAY STRAIGHT W/COVER

SN	DIMENSION TABLE	QTY
04	W=450mm, H=50mm, T=1.5mm & L=3000mm	37
05	W=600mm, H=50mm, T=2.0mm & L=3000mm	17

DRAWN BY	SHAH ALAM	
CHECKED BY	AMIR KHAN	
APPROVED BY	NASSER ANANI	
DATE	04/05/2026	
REF NO. :		
CONSULTANT :		

TITLE: CABLE TRAY STRAIGHT W/COVER

CLIENT: SITE TECHNOLOGY INTEGRATED SYSTEM LLC

SEC ITEM NO:

BONN METAL CONS. IND.


BONN GROUP OF COMPANIES
Cable Management Systems

DWRG. NO. :


SHEET NO. :

SCALE: NTS

REV. 01

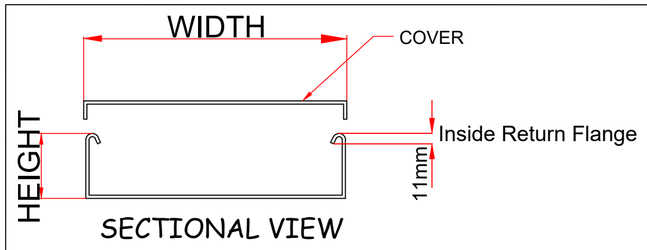

NOTE:-MATERIAL FINISH HDG

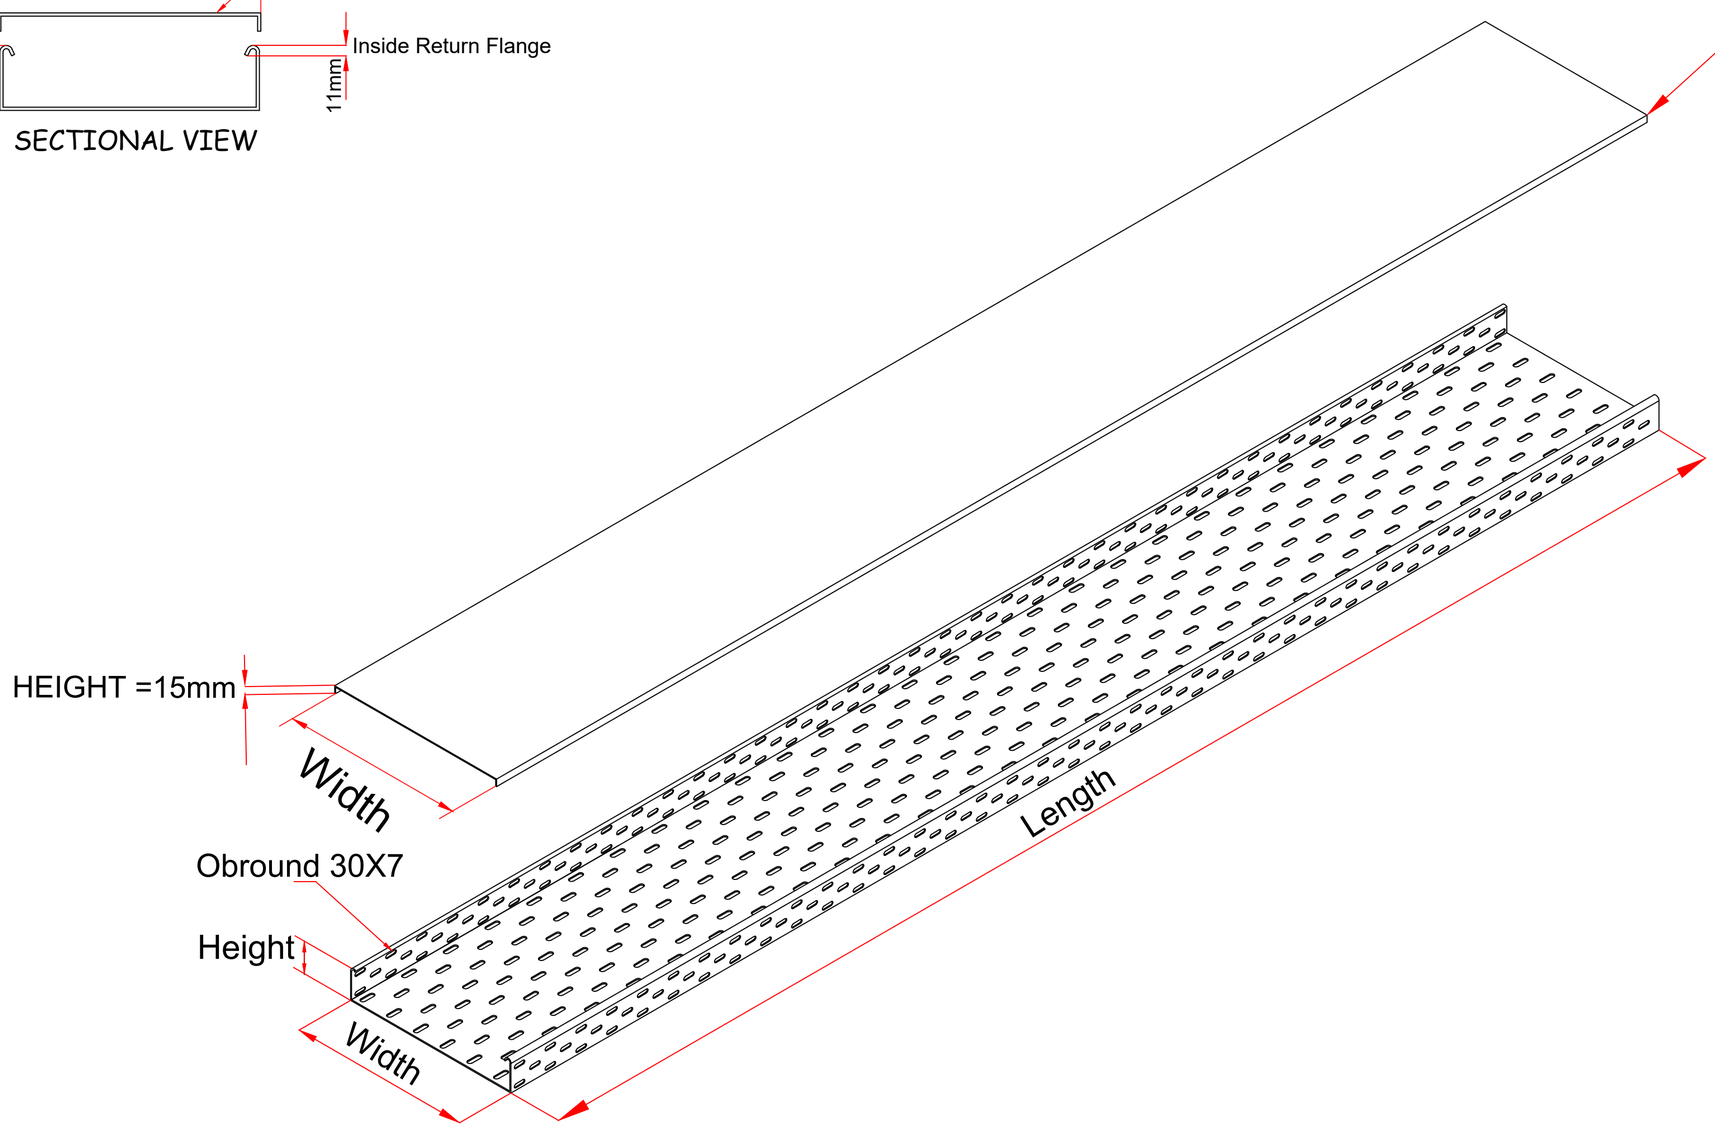



CABLE TRAY STRAIGHT W/COVER

SN.	DIMENSION TABLE	QTY				
06	W=750mm, H=75mm, T=2.0mm & L=3000mm	12	DRAWN BY	SHAH ALAM		TITLE: CABLE TRAY STRAIGHT W/COVER
			CHECKED BY	AMIR KHAN		BONN METAL CONS. IND.
			APPROVED BY	NASSER ANANI		CLIENT: SITE TECHNOLOGY INTEGRATED SYSTEM LLC
			DATE	04/05/2026		
			REF NO. :			SEC ITEM NO:
			CONSULTANT :			DWRG. NO. : / SHEET NO. : / SCALE: NTS / REV. 00

BONN GROUP OF COMPANIES
Cable Management Systems

NOTE:-MATERIAL FINISH HDG

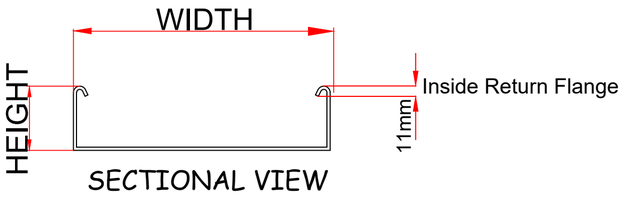

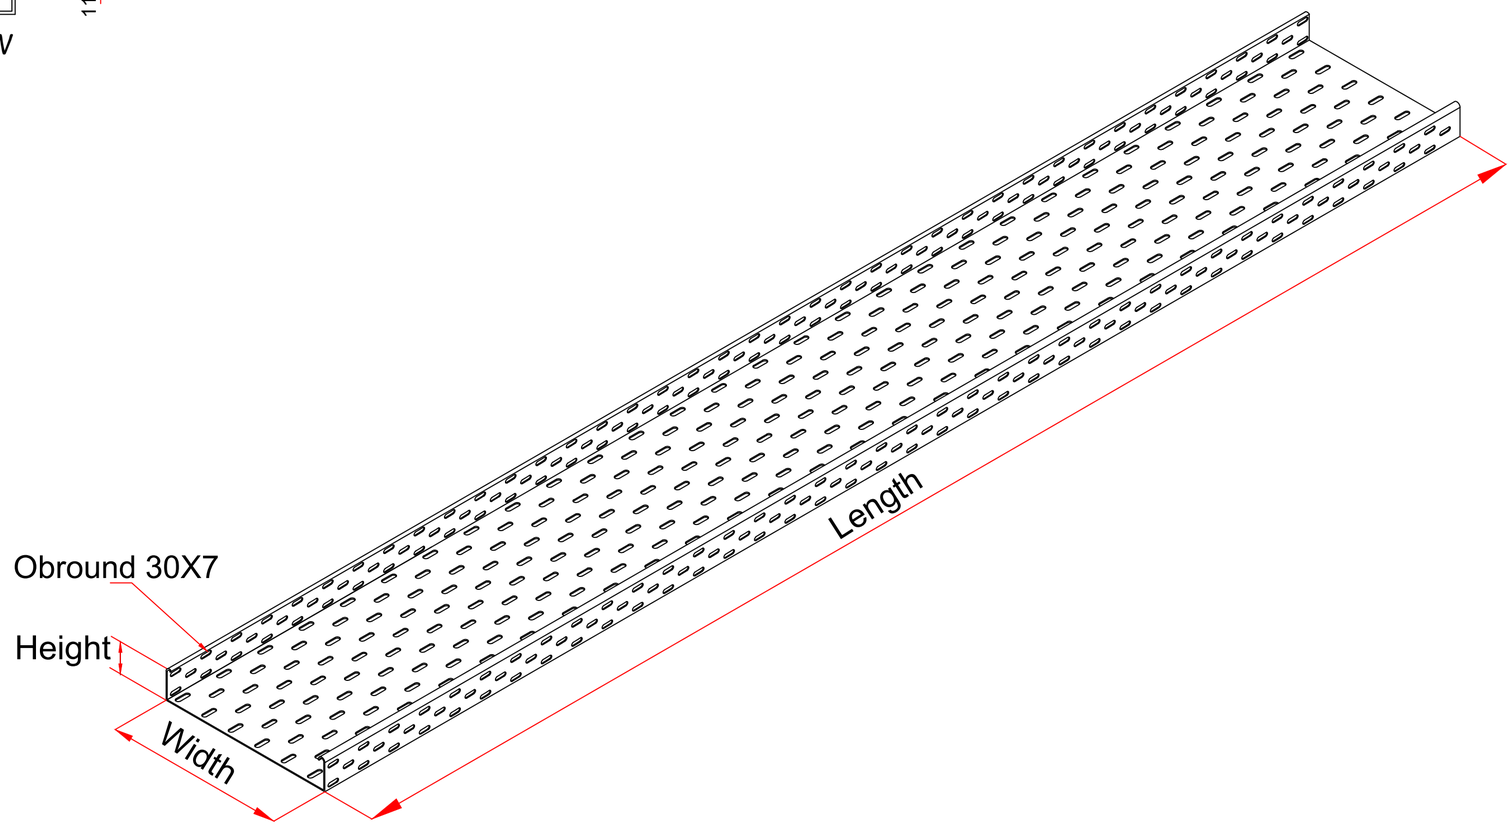

CABLE TRAY STRAIGHT

SN.	DIMENSION TABLE	QTY			
07	W=900mm, H=75mm, T=2.0mm & L=3000mm	17			

DRAWN BY	SHAH ALAM	
CHECKED BY	AMIR KHAN	
APPROVED BY	NASSER ANANI	
DATE	04/05/2026	
REF NO. :		
CONSULTANT :		

TITLE: CABLE TRAY STRAIGHT

CLIENT: SITE TECHNOLOGY INTEGRATED SYSTEM LLC

SEC ITEM NO:

BONN METAL CONS. IND.

BONN GROUP OF COMPANIES
Cable Management Systems


DWRG. NO. :

SHEET NO. :

SCALE: NTS

REV. 00

NOTE:-MATERIAL FINISH HDG

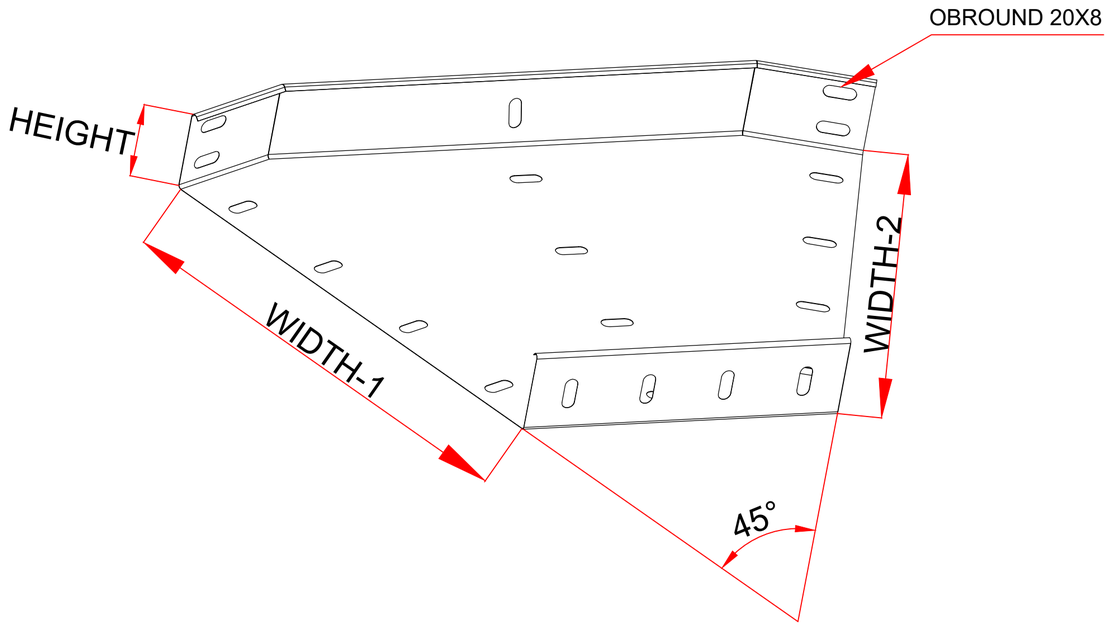

CABLE TRAY BEND 45DEG

SN	DIMENSION TABLE	QTY
08	W=900mm, H=75mm, T=2.0mm	03

DRAWN BY	SHAH ALAM	
CHECKED BY	AMIR KHAN	
APPROVED BY	NASSER ANANI	
DATE	04/05/2026	
REF NO. :		
CONSULTANT :		

TITLE: CABLE TRAY BEND 45DEG

CLIENT:SITE TECHNOLOGY INTEGRATED SYSTEM LLC

SEC ITEM NO:


BONN METAL CONS. IND.

BONN GROUP OF COMPANIES

Cable Management Systems

DWRG. NO. :		REV. 01
SHEET NO. :	SCALE: NTS	

NOTE:-MATERIAL FINISH HDG

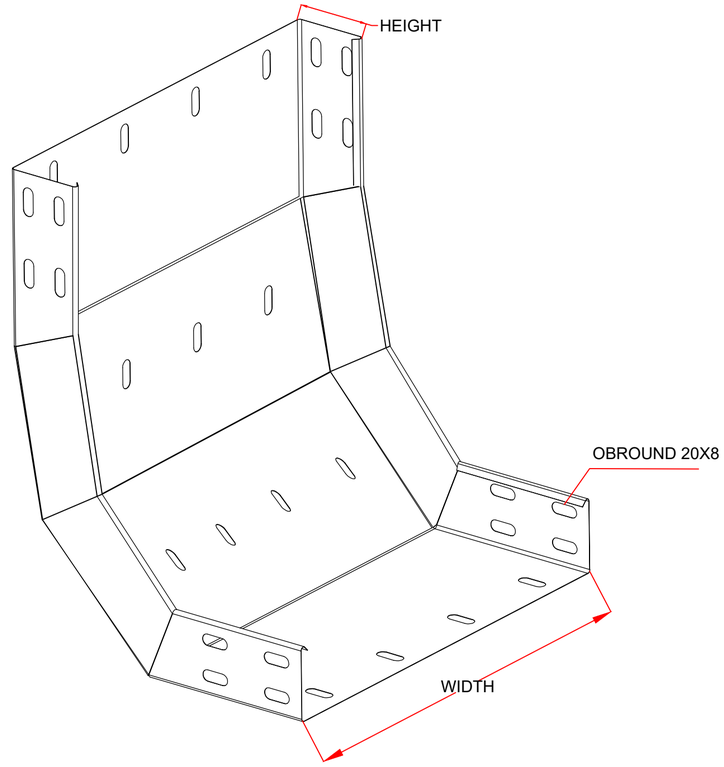


CABLE TRAY ADJUSTABLE INSIDE RISER

SN	DIMENSION TABLE	QTY	DRAWN BY	SHAH ALAM		TITLE: CABLE TRAY ADJUSTABLE INSIDE RISER	BONN METAL CONS. IND.		
09	W=900mm, H=75mm, T=2.0mm	02	CHECKED BY	AMIR KHAN					
			APPROVED BY	NASSER ANANI		CLIENT: SITE TECHNOLOGY INTEGRATED SYSTEM LLC			
			DATE	04/05/2026					
			REF NO. :			SEC ITEM NO:	DWRG. NO. :		REV.
			CONSULTANT :				SHEET NO. :	SCALE: NTS	00

BONN GROUP OF COMPANIES
Cable Management Systems

NOTE:-MATERIAL FINISH HDG

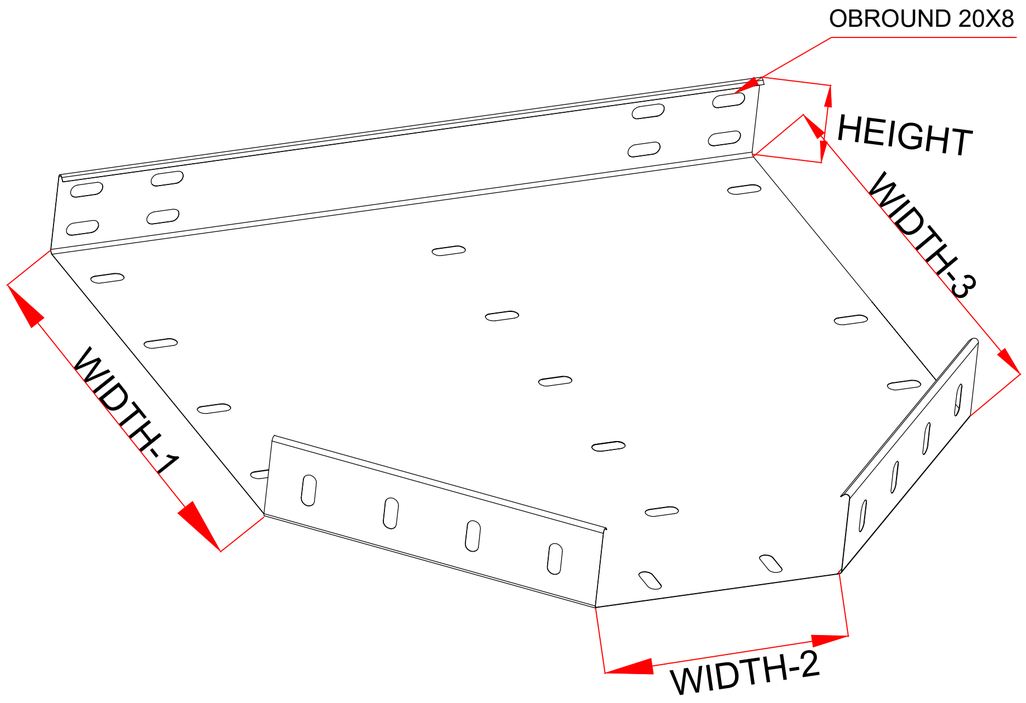

CABLE TRAY UNEQUAL TEE

SN	DIMENSION TABLE	QTY
10	W1=W3=900mm, W2=300mm H=50mm, T=2.0mm	02
16	W1=W3=300mm, W2=150mm H=50mm, T=2.0mm	10
21	W1=W3=750mm, W2=450mm H=50mm, T=2.0mm	02

DRAWN BY	SHAH ALAM	
CHECKED BY	AMIR KHAN	
APPROVED BY	NASSER ANANI	
DATE	04/05/2026	
REF NO. :		
CONSULTANT :		

TITLE: CABLE TRAY UNEQUAL TEE

CLIENT: SITE TECHNOLOGY INTEGRATED SYSTEM LLC

SEC ITEM NO:

BONN METAL CONS. IND.

BONN GROUP OF COMPANIES
Cable Management Systems


DWRG. NO. :

SHEET NO. :

SCALE: NTS

REV. 01

NOTE:-MATERIAL FINISH HDG

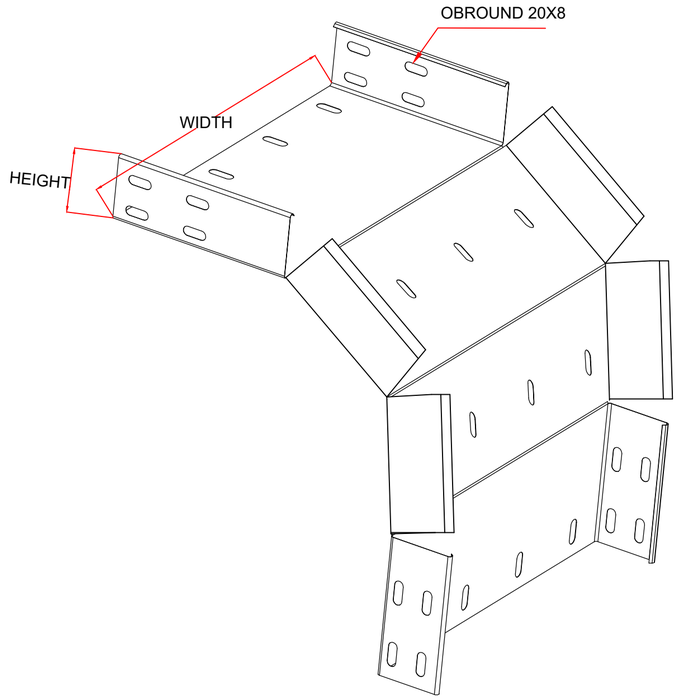

CABLE TRAY ADJUSTABLE OUTSIDE RISER

SN	DIMENSION TABLE	QTY
11	W=300mm, H=50mm, T=2.0mm	20
27	W=225mm, H=50mm, T=2.0mm	15
30	W=225mm, H=50mm, T=2.0mm	19

DRAWN BY	SHAH ALAM	
CHECKED BY	AMIR KHAN	
APPROVED BY	NASSER ANANI	
DATE	04/05/2026	
REF NO. :		
CONSULTANT :		

TITLE: CABLE TRAY ADJUSTABLE OUTSIDE RISER

CLIENT:

SEC ITEM NO:

BONN METAL CONS. IND.

Cable Management Systems


DWRG. NO. :

REV. 00

SHEET NO. :

SCALE: NTS

NOTE:- MATERIAL FINISH HDG

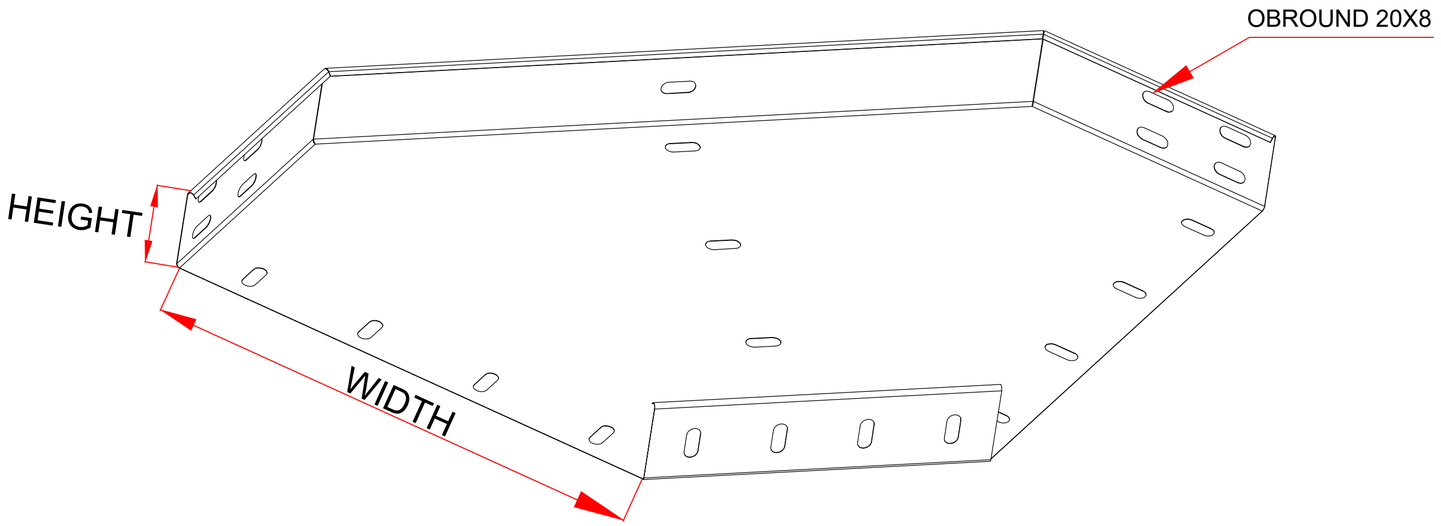

CABLE TRAY BEND 90DEG

SN	DIMENSIONS TABLE	QTY
12	W=300mm, H=50mm, T=2.0mm	15
29	W=225mm, H=50mm, T=2.0mm	19

DRAWN BY	SHAH ALAM	
CHECKED BY	AMIR KHAN	
APPROVED BY	NASSER ANANI	
DATE	04/05/2026	
REF NO. :		
CONSULTANT :		

TITLE: CABLE TRAY BEND90DEG

CLIENT: SITE TECHNOLOGY INTEGRATED SYSTEM LLC

BONN METAL CONS. IND.

BONN GROUP OF COMPANIES
Cable Management Systems

SEC ITEM NO:


DWRG. NO. :

SHEET NO. :

SCALE: NTS

REV. 00

NOTE:-MATERIAL FINISH HDG

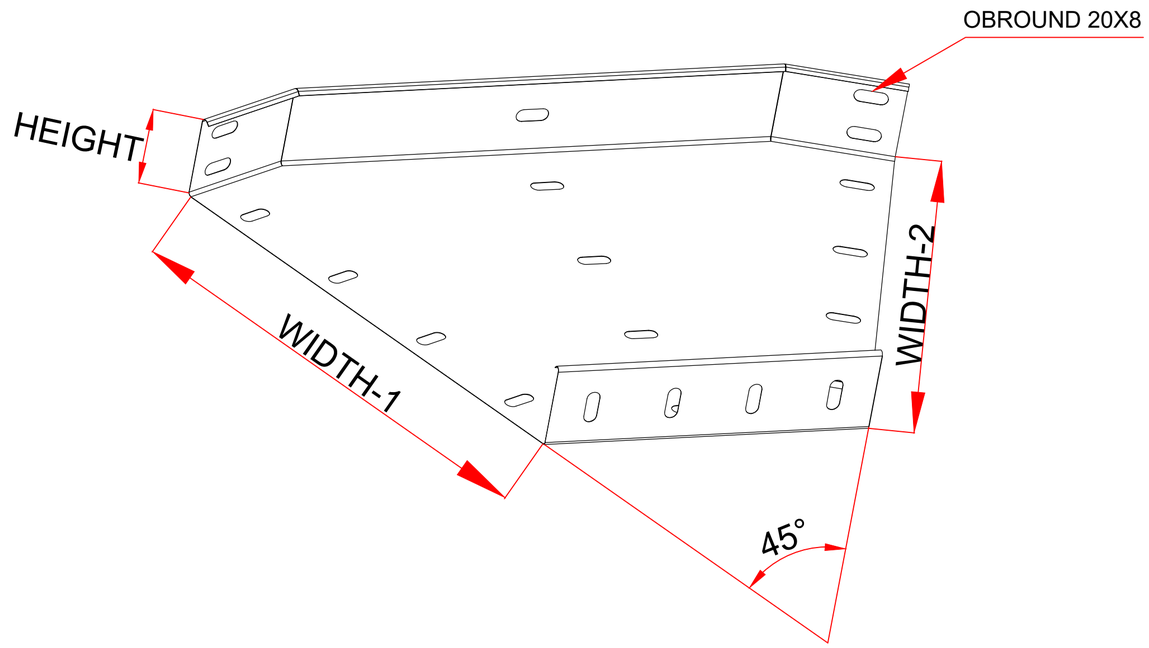


CABLE TRAY BEND 45DEG

SN	DIMENSION TABLE	QTY	DRAWN BY	SHAH ALAM		TITLE: CABLE TRAY BEND 45DEG	BONN METAL CONS. IND.	
13	W=300mm, H=50mm, T=2.0mm	15	CHECKED BY	AMIR KHAN				
			APPROVED BY	NASSER ANANI		CLIENT:SITE TECHNOLOGY INTEGRATED SYSTEM LLC		
			DATE	04/05/2026				
			REF NO. :			SEC ITEM NO:	DWRG. NO. :	REV. 01
			CONSULTANT :				SHEET NO. : / SCALE: NTS	

BONN GROUP OF COMPANIES
Cable Management Systems

NOTE:- MATERIAL FINISH HDG

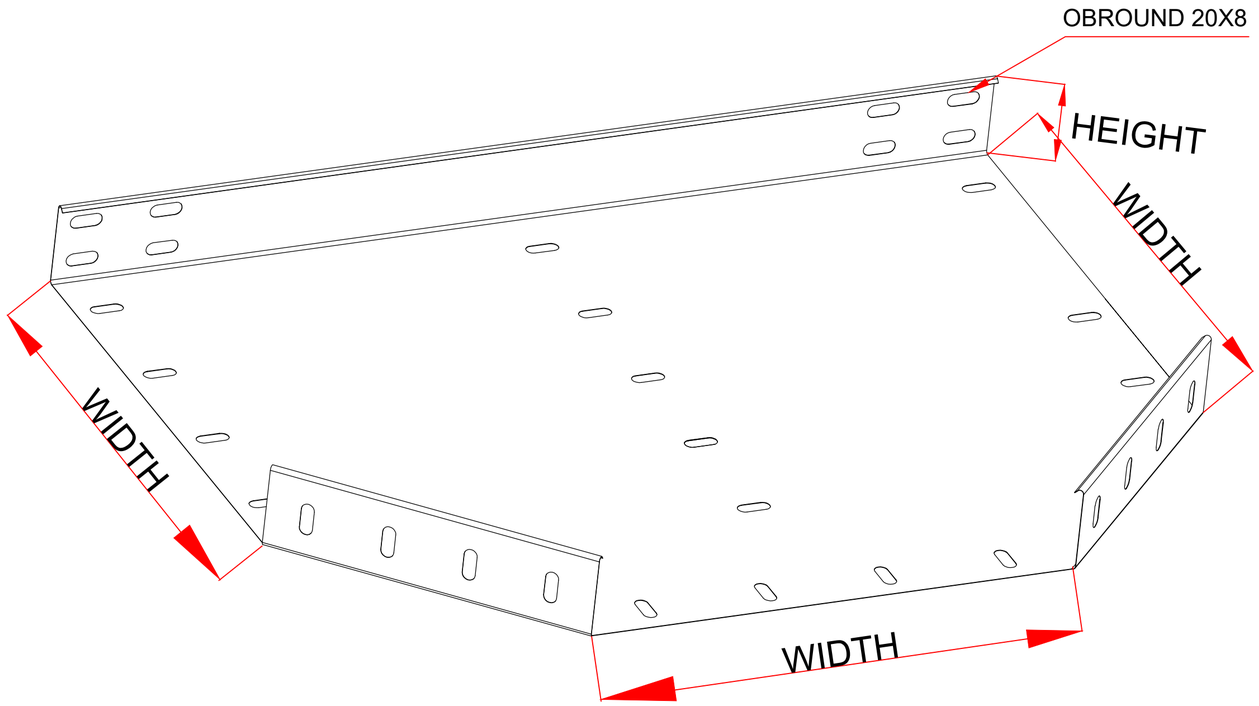

CABLE TRAY EQUAL TEE

SN	DIMENSION TABLE	QTY
14	W=300mm, H=50mm, T=2.0mm	15
31	W=225mm, H=50mm, T=2.0mm	30

DRAWN BY	SHAH ALAM	
CHECKED BY	AMIR KHAN	
APPROVED BY	NASSER ANANI	
DATE	04/05/2026	
REF NO. :		
CONSULTANT :		

TITLE: CABLE TRAY EQUAL TEE

CLIENT: SITE TECHNOLOGY INTEGRATED SYSTEM LLC

SEC ITEM NO:

BONN METAL CONS. IND.

BONN GROUP OF COMPANIES
Cable Management Systems


DWRG. NO. :

SHEET NO. :

SCALE: NTS

REV. 01

NOTE:- MATERIAL FINISH HDG

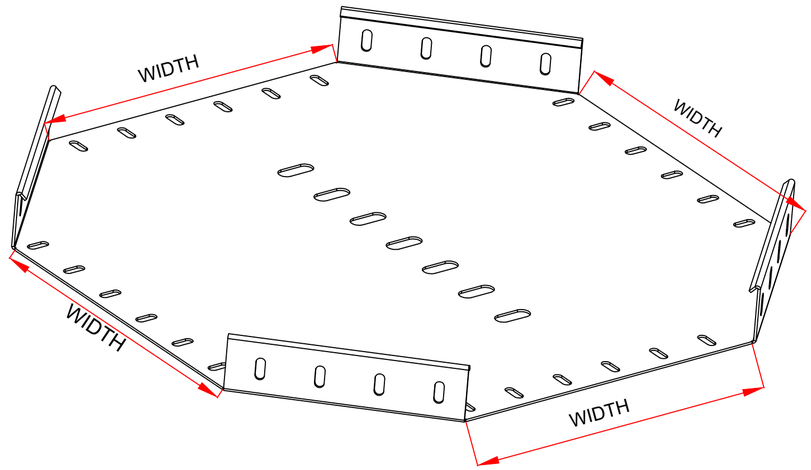

CABLE TRAY EQUAL CROSS

SN	DIMENSION TABLE	QTY
15	W=300mm, H=50mm, T=2.0mm	10

DRAWN BY	SHAH ALAM	
CHECKED BY	AMIR KHAN	
APPROVED BY	NASSER ANANI	
DATE	04/05/2026	
REF NO. :		
CONSULTANT :		

TITLE: CABLE TRAY EQUAL CROSS

CLIENT: SITE TECHNOLOGY INTEGRATED SYSTEM LLC

BONN METAL CONS. IND.

BONN GROUP OF COMPANIES
Cable Management Systems

SEC ITEM NO:


DWRG. NO. :

SHEET NO. :

SCALE: NTS

REV. 01

NOTE:-MATERIAL FINISH HDG

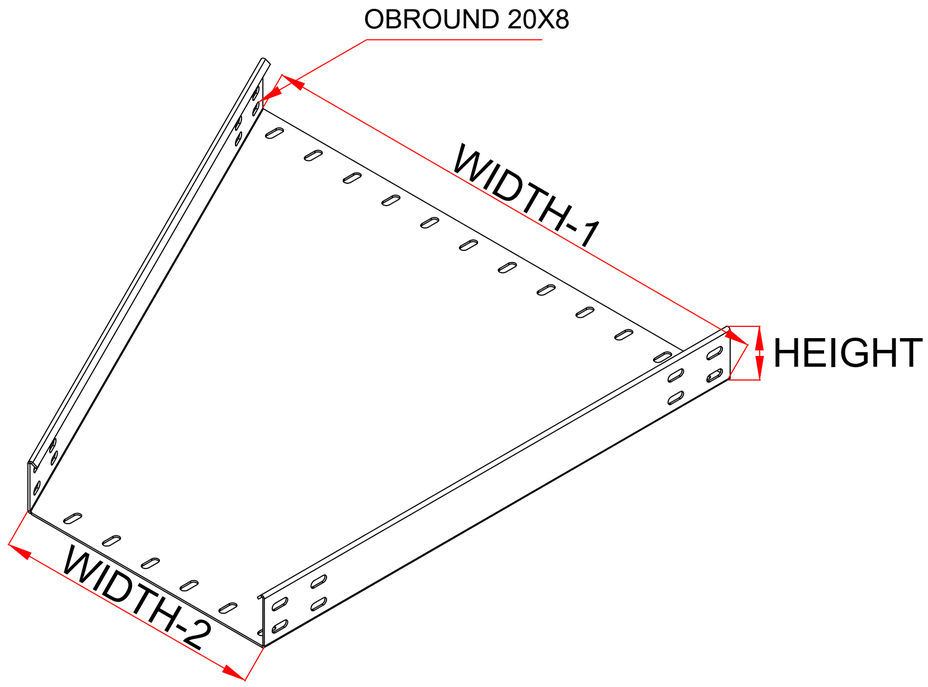

CABLE TRAY STRAIGHT REDUCER

SN	DIMENSION TABLE	QTY
17	W1=300mm, W2=150mm, H=50mm & T=2.0mm	10
32	W1=225mm, W2=150mm, H=50mm & T=2.0mm	10

DRAWN BY	SHAH ALAM	
CHECKED BY	AMIR KHAN	
APPROVED BY	NASSER ANANI	
DATE	04/05/2026	
REF NO. :		
CONSULTANT :		

TITLE: CABLE TRAY STRAIGHT REDUCER

CLIENT: SITE TECHNOLOGY INTEGRATED SYSTEM LLC

SEC ITEM NO:

BONN METAL CONS. IND.

BONN GROUP OF COMPANIES
Cable Management Systems


DWRG. NO. :

SHEET NO. :

SCALE: NTS

REV. 01

NOTE:- MATERIAL FINISH HDG

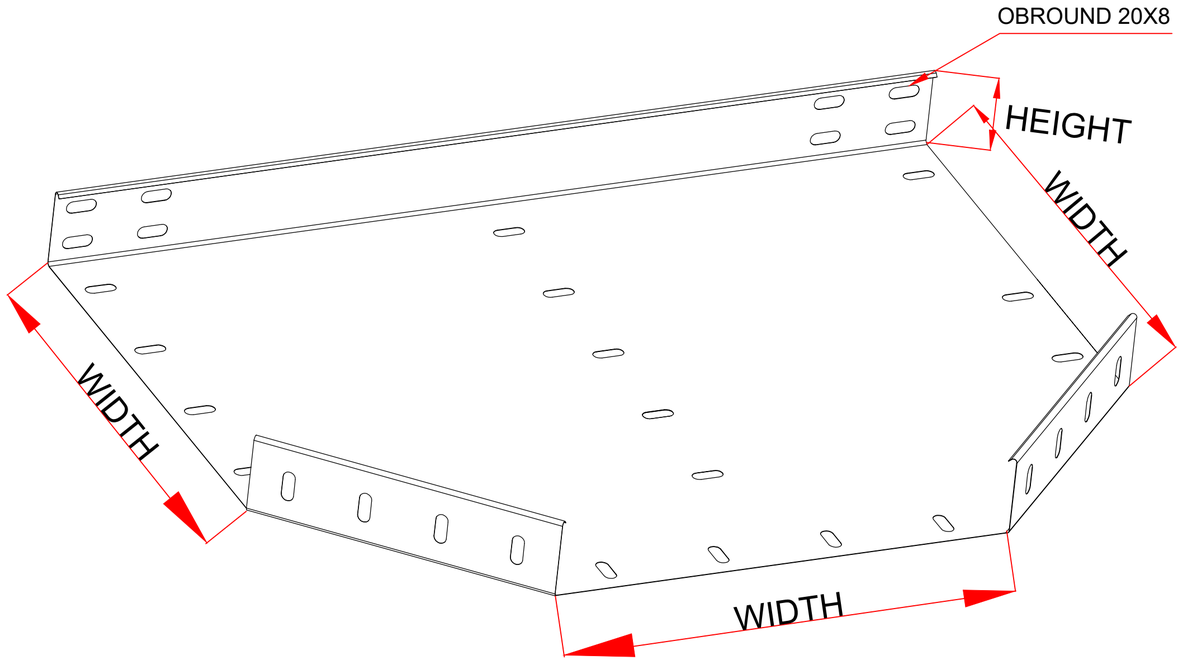

CABLE TRAY EQUAL TEE

SN	DIMENSION TABLE	QTY
18	W=150mm, H=50mm, T=2.0mm	10
24	W=450mm, H=50mm, T=2.0mm	05

DRAWN BY	SHAH ALAM	
CHECKED BY	AMIR KHAN	
APPROVED BY	NASSER ANANI	
DATE	04/05/2026	
REF NO. :		
CONSULTANT :		

TITLE: CABLE TRAY EQUAL TEE

CLIENT: SITE TECHNOLOGY INTEGRATED SYSTEM LLC

SEC ITEM NO:

BONN METAL CONS. IND.

BONN GROUP OF COMPANIES
Cable Management Systems


DWRG. NO. :

SHEET NO. :

SCALE: NTS

REV. 01

NOTE:-MATERIAL FINISH HDG

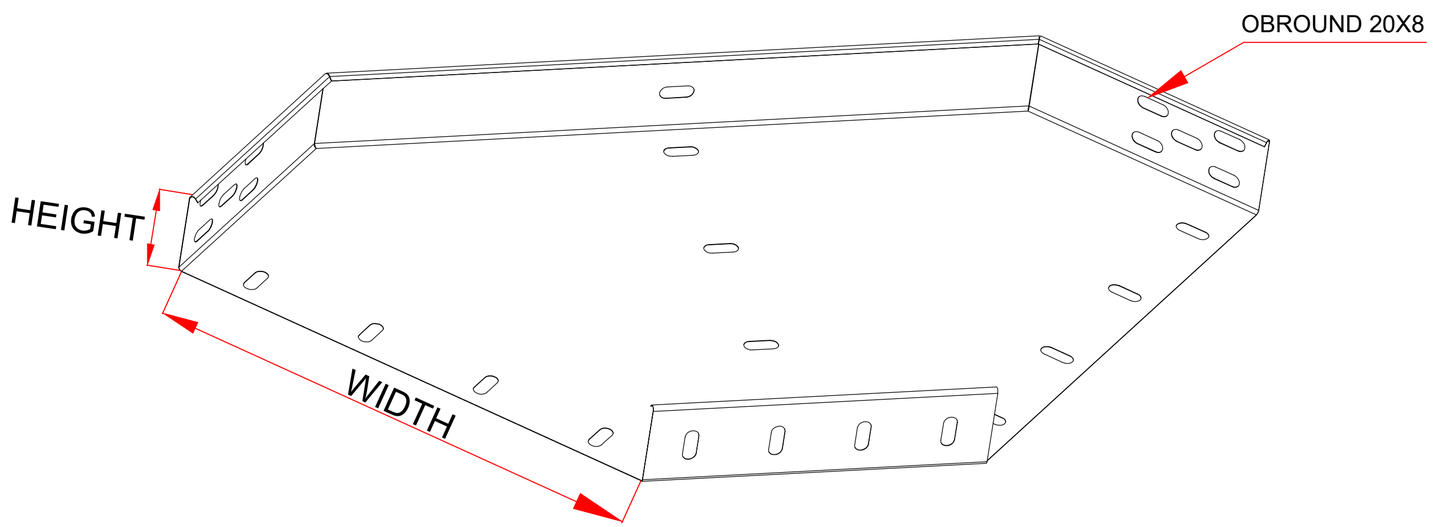

CABLE TRAY BEND 90DEG

SN	DIMENSION TABLE	QTY
19	W=150mm, H=50mm, T=2.0mm	10
28	W=225mm, H=50mm, T=2.0mm	10

DRAWN BY	SHAH ALAM	
CHECKED BY	AMIR KHAN	
APPROVED BY	NASSER ANANI	
DATE	04/05/2026	
REF NO. :		
CONSULTANT :		

TITLE: CABLE TRAY E BEND 90DEG

CLIENT: SITE TECHNOLOGY INTEGRATED SYSTEM LLC

SEC ITEM NO:

BONN METAL CONS. IND.

BONN GROUP OF COMPANIES
Cable Management Systems


DWRG. NO. :

SHEET NO. :

SCALE: NTS

REV. 01

NOTE:-MATERIAL FINISH HDG

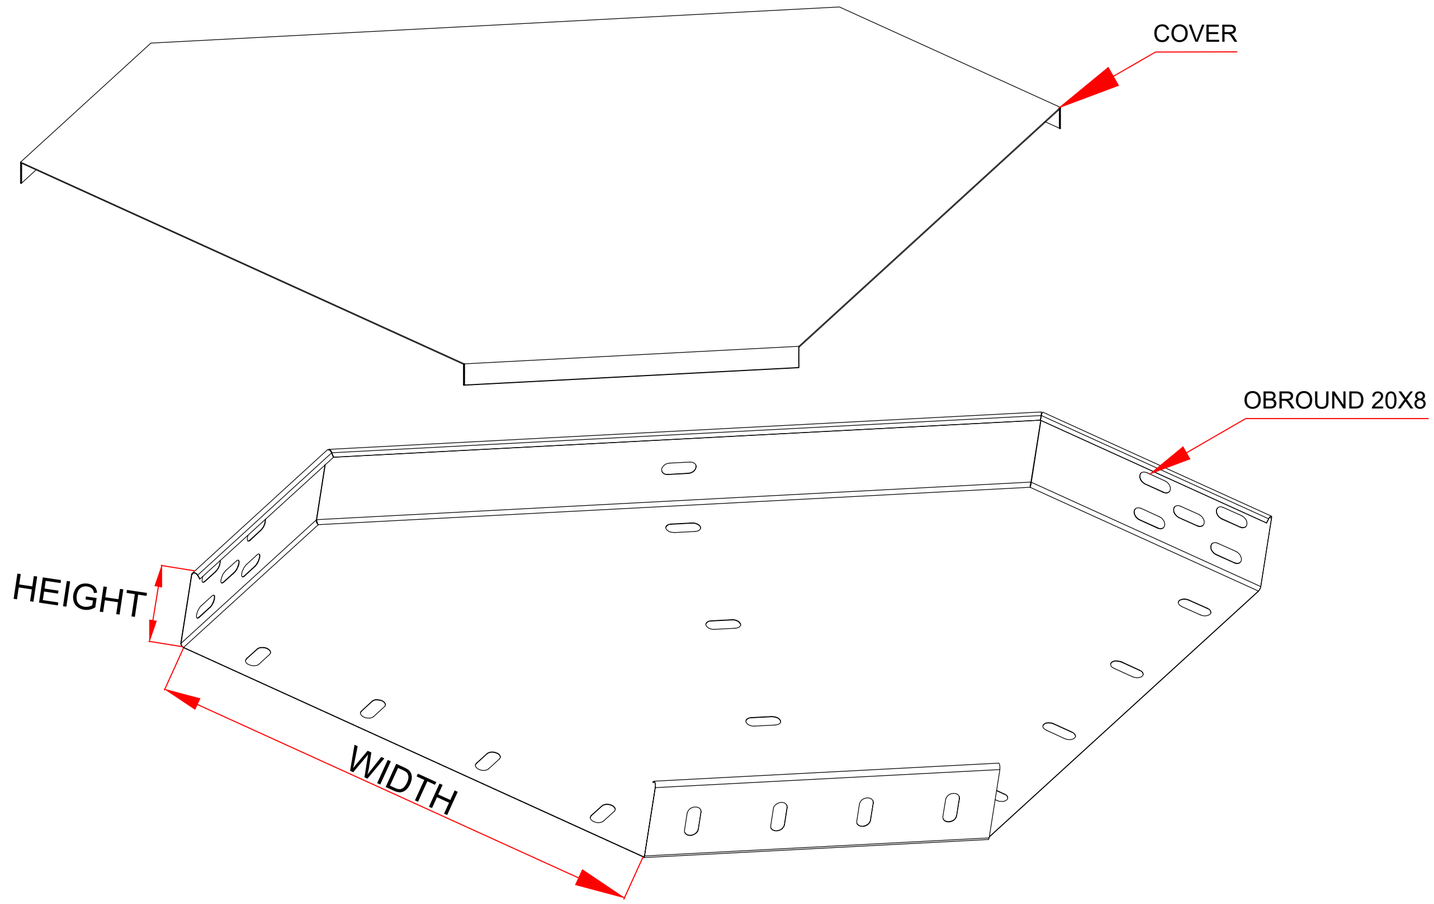

CABLE TRAY BEND 90DEG W/COVER

SN	DIMENSION TABLE	QTY	DRAWN BY	SHAH ALAM	
20	W=750mm, H=75mm, T=2.0mm	04	CHECKED BY	AMIR KHAN	
			APPROVED BY	NASSER ANANI	
			DATE	04/05/2026	
			REF NO. :		
			CONSULTANT :		

TITLE: CABLE TRAY BEND 90DEG W/COVER

CLIENT: SITE TECHNOLOGY INTEGRATED SYSTEM LLC

SEC ITEM NO:

BONN METAL CONS. IND.

BONN GROUP OF COMPANIES
Cable Management Systems


DWRG. NO. :

SHEET NO. :

SCALE: NTS

REV. 01

NOTE:-MATERIAL FINISH HDG

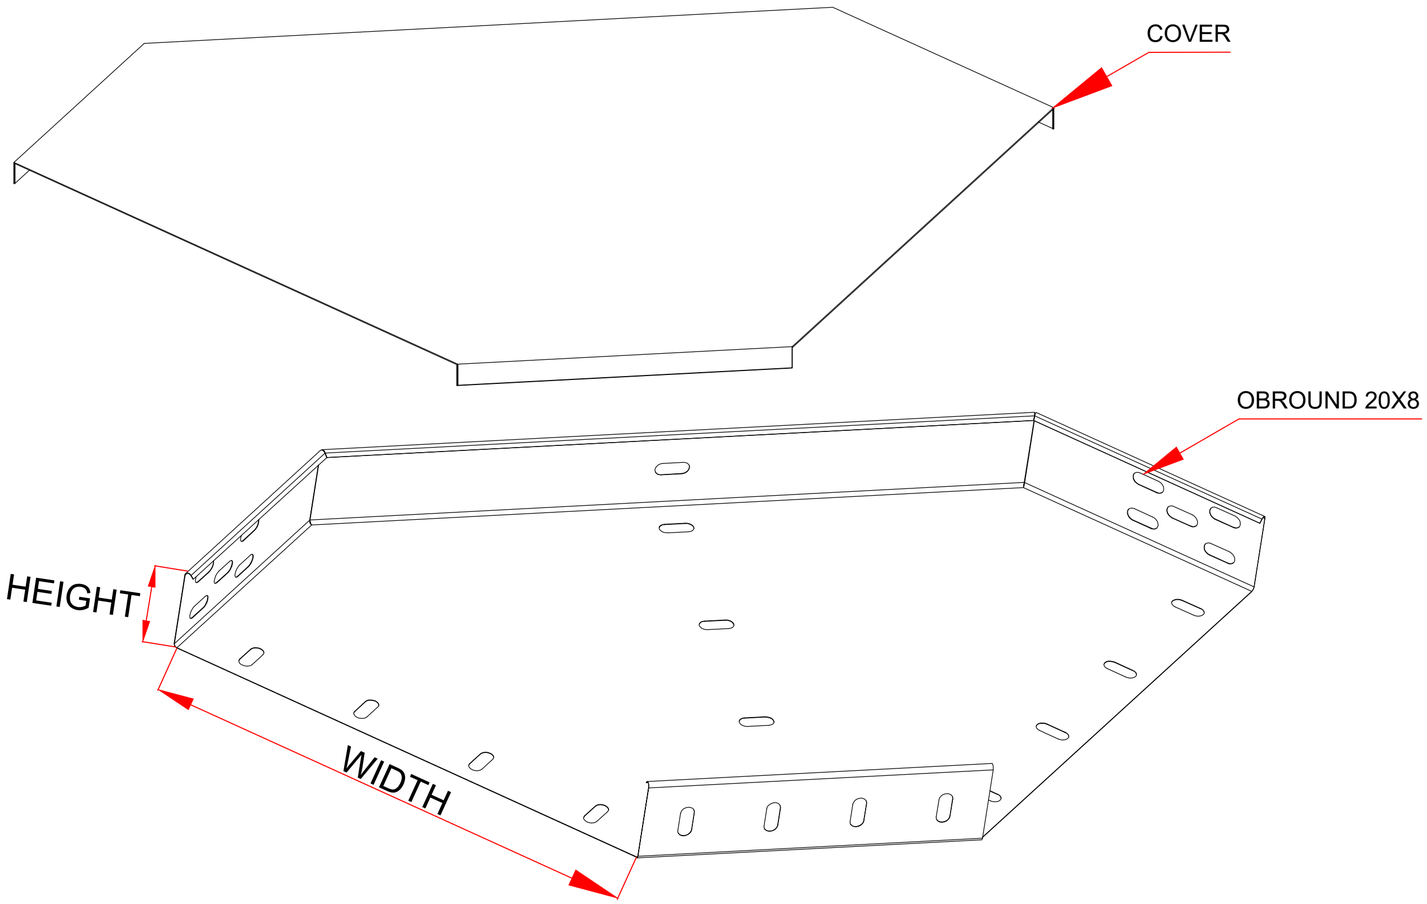

CABLE TRAY BEND 90DEG W/COVER

SN	DIMENSION TABLE	QTY
22	W=450mm, H=50mm, T=2.0mm	10
26	W=600mm, H=50mm, T=2.0mm	04

DRAWN BY	SHAH ALAM	
CHECKED BY	AMIR KHAN	
APPROVED BY	NASSER ANANI	
DATE	04/05/2026	
REF NO. :		
CONSULTANT :		

TITLE: CABLE TRAY BEND 90DEG

CLIENT: SITE TECHNOLOGY INTEGRATED SYSTEM LLC

SEC ITEM NO:

BONN METAL CONS. IND.

BONN GROUP OF COMPANIES
Cable Management Systems


DWRG. NO. :

SHEET NO. :

SCALE: NTS

REV. 01

NOTE:- MATERIAL FINISH HDG

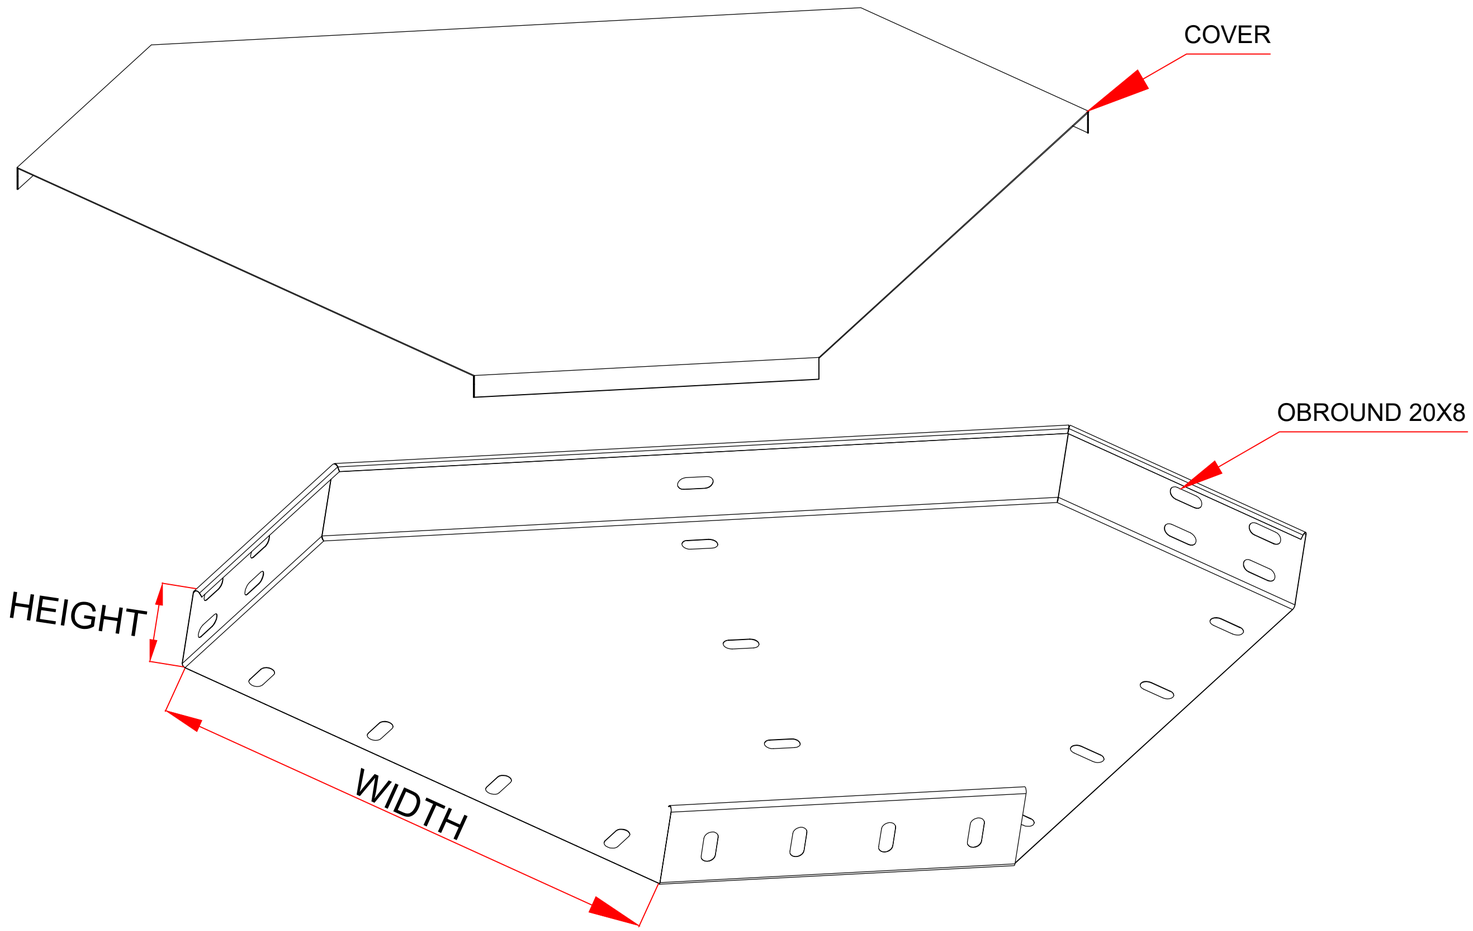

CABLE TRAY BEND 90DEG W/COVER

SN	DIMENSION TABLE	QTY
23	W=450mm, H=50mm, T=2.0mm	10
25	W=600mm, H=50mm, T=2.0mm	08

DRAWN BY	SHAH ALAM	
CHECKED BY	AMIR KHAN	
APPROVED BY	NASSER ANANI	
DATE	04/05/2026	
REF NO. :		
CONSULTANT :		

TITLE: CABLE TRAY BEND 90DEG W/COVER

CLIENT: SITE TECHNOLOGY INTEGRATED SYSTEM LLC

SEC ITEM NO:

BONN METAL CONS. IND.

BONN GROUP OF COMPANIES
Cable Management Systems


DWRG. NO. :

SHEET NO. :

SCALE: NTS

REV. 01

NOTE:- MATERIAL FINISH HDG

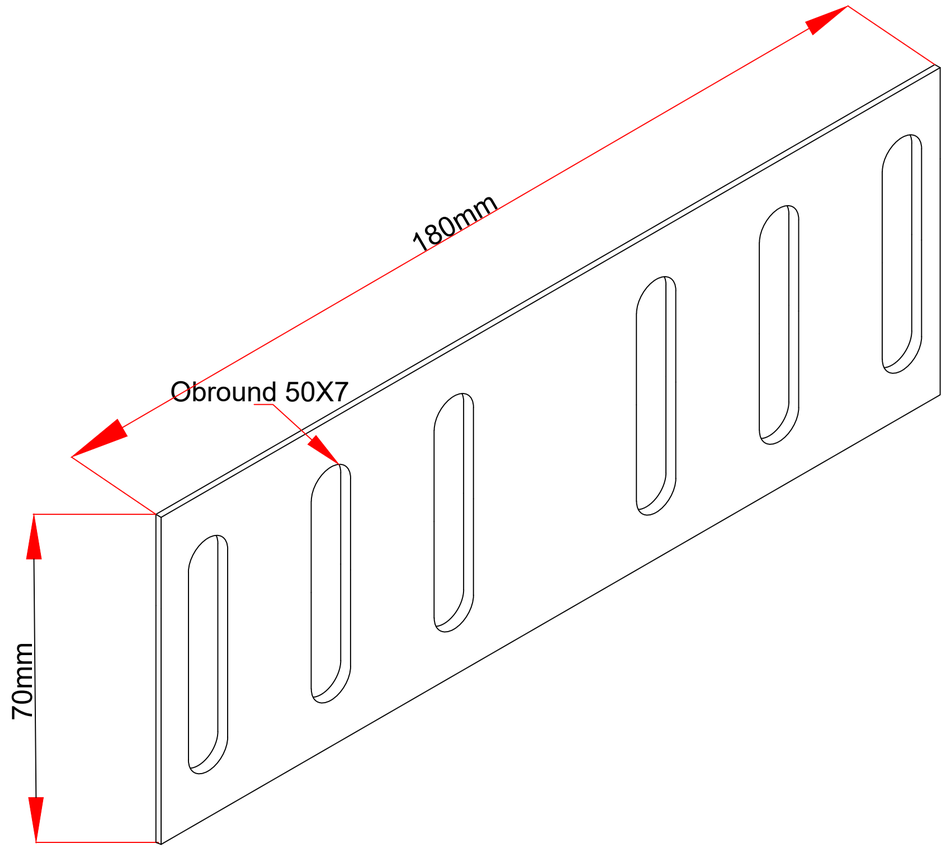

CABLE TRAY STRAIGHT COUPLER

SN	DIMENSION TABLE	QTY
33	H=75, T=2.0mm	200

DRAWN BY	SHAH ALAM	
CHECKED BY	AMIR KHAN	
APPROVED BY	NASSER ANANI	
DATE	04/05/2026	
REF NO. :		
CONSULTANT :		

TITLE: CABLE TRAY STRAIGHT COUPLER

CLIENT: SITE TECHNOLOGY INTEGRATED SYSTEM LLC

SEC ITEM NO:

BONN METAL CONS. IND.

BONN GROUP OF COMPANIES
Cable Management Systems


DWRG. NO. :

SHEET NO. :

SCALE: NTS

REV. 01

NOTE:-MATERIAL FINISH HDG

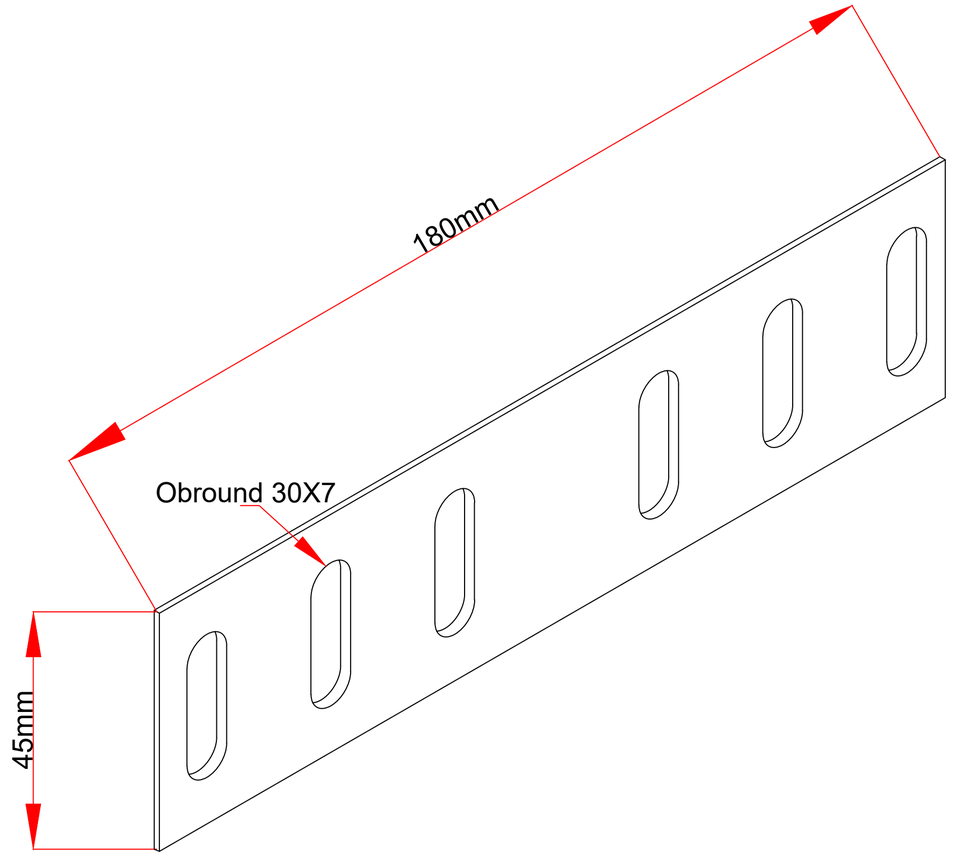

CABLE TRAY STRAIGHT COUPLER

SN	DIMENSION TABLE	QTY
34	H=50, T=2.0mm	200

DRAWN BY	SHAH ALAM	
CHECKED BY	AMIR KHAN	
APPROVED BY	NASSER ANANI	
DATE	04/05/2026	
REF NO. :		
CONSULTANT :		

TITLE: CABLE TRAY STRAIGHT COUPLER

CLIENT: SITE TECHNOLOGY INTEGRATED SYSTEM LLC

SEC ITEM NO:

BONN METAL CONS. IND.

BONN GROUP OF COMPANIES
Cable Management Systems


DWRG. NO. :


SHEET NO. :

SCALE: NTS

REV. 01

NOTE:-MATERIAL FINISH GI

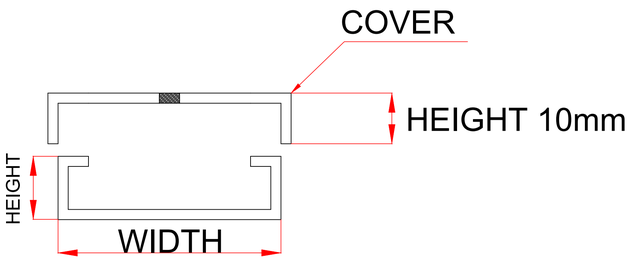

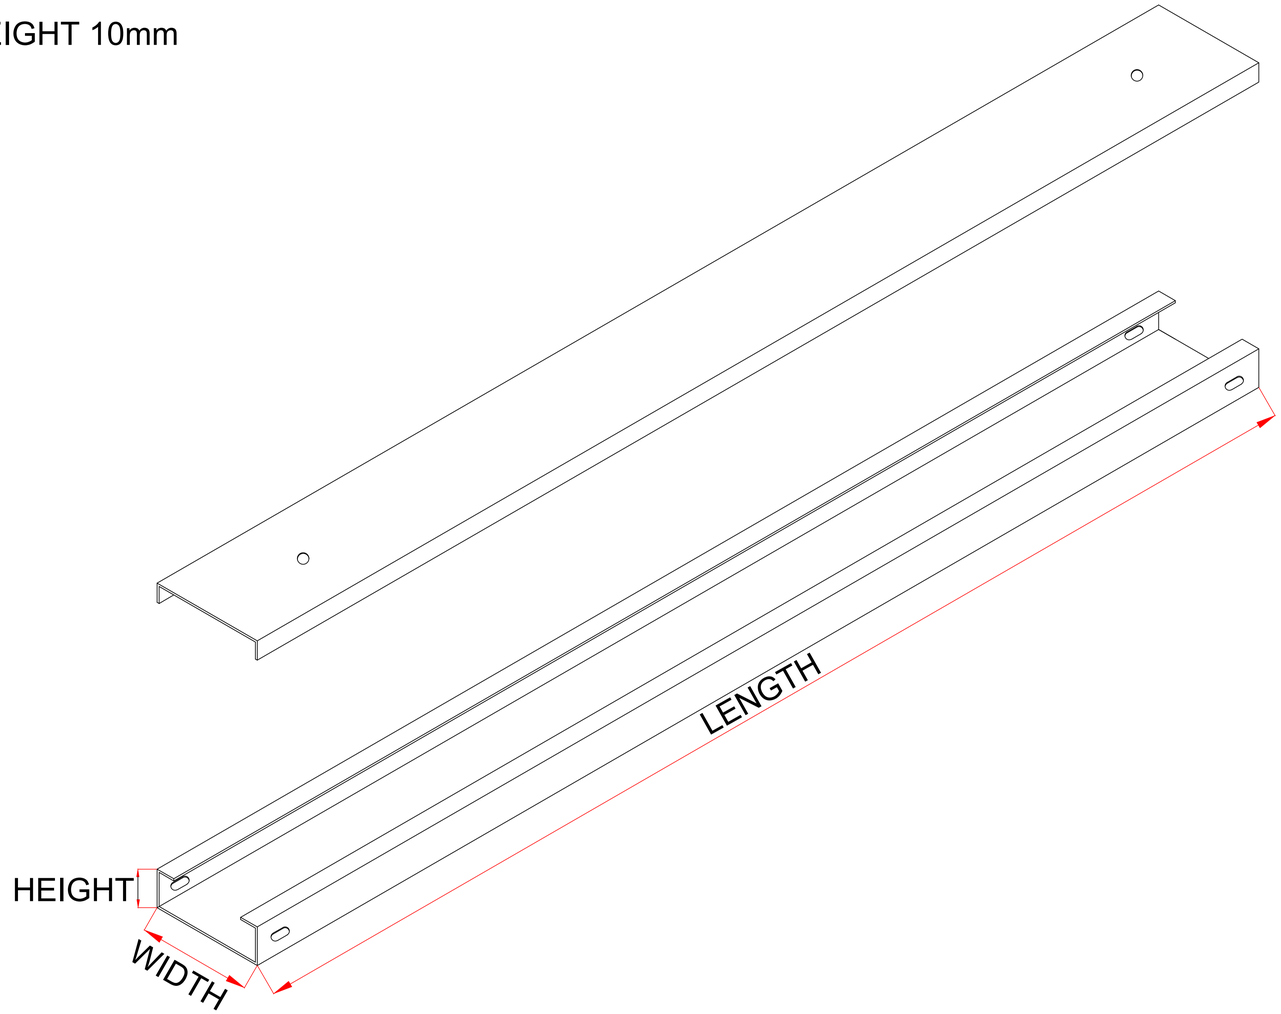

CABLE TRUNKING W/COVER

SN	DIMENSION TABLE	QTY
37	W=50mm, H=50mm, T=1.2mm & L=3000mm	167

DRAWN BY	SHAH ALAM	
CHECKED BY	AMIR KHAN	
APPROVED BY	NASSER ANANI	
DATE	04/05/2026	
REF NO. :		
CONSULTANT :		

TITLE: CABLE TRUNKING W/COVER

CLIENT: SITE TECHNOLOGY INTEGRATED SYSTEM LLC

BONN METAL CONS. IND.

BONN GROUP OF COMPANIES
Cable Management Systems

SEC ITEM NO:


DWRG. NO. :


SHEET NO. :

SCALE: NTS

REV. 01

NOTE:-MATERIAL FINISH GI

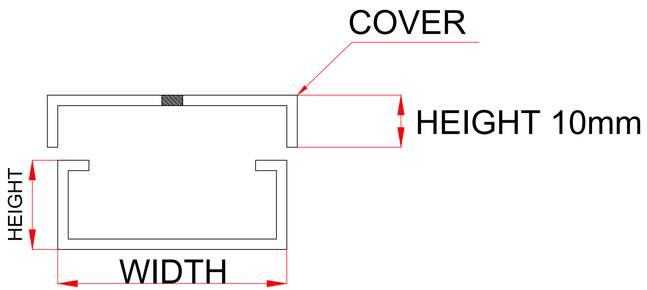

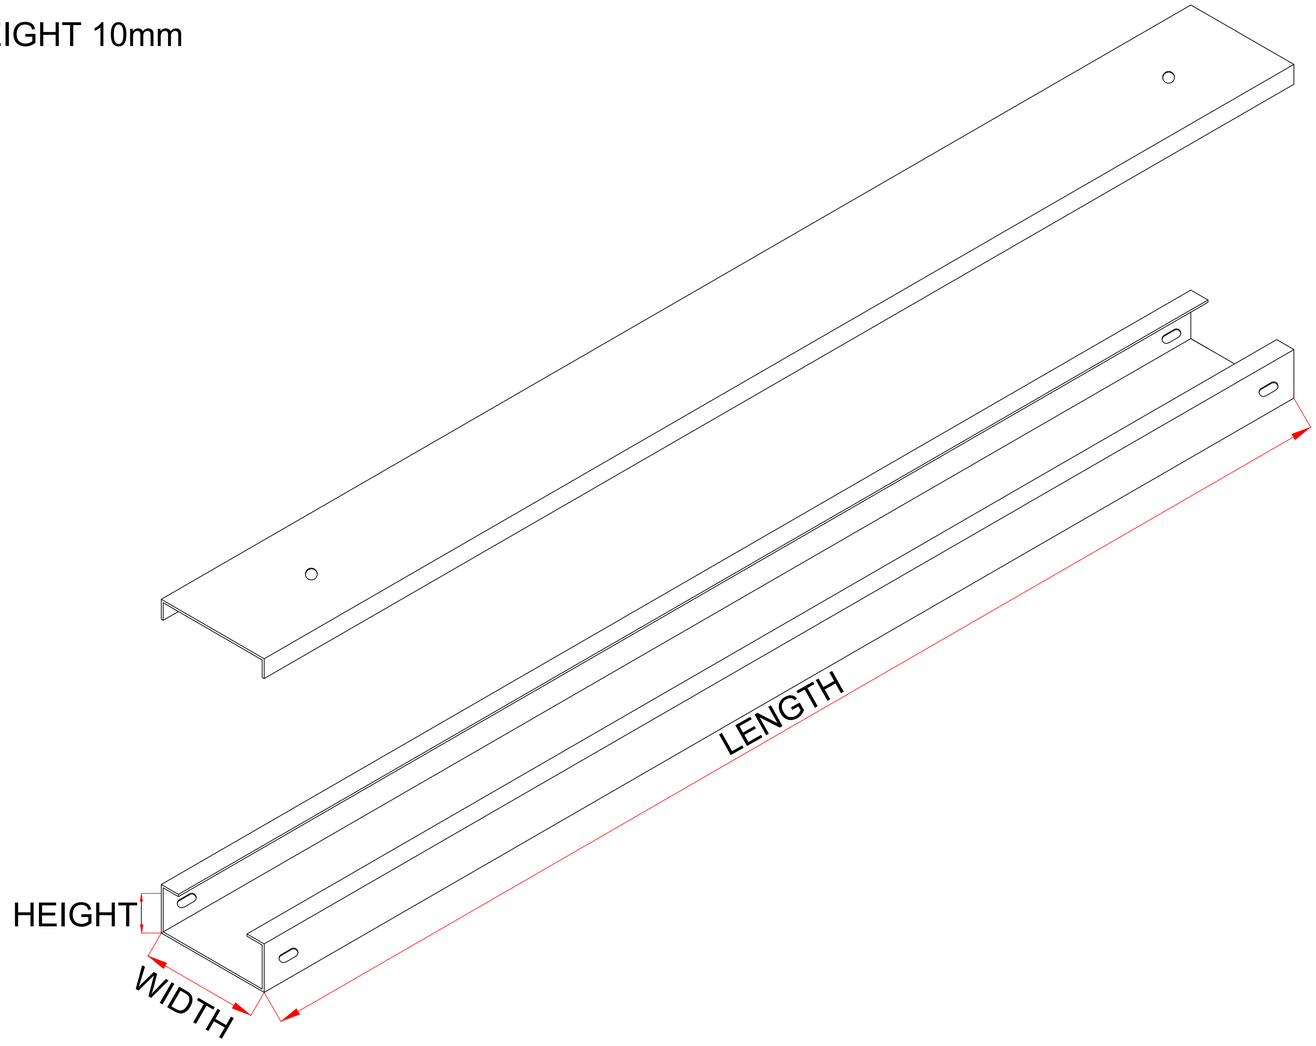

CABLE TRUNKING W/COVER

SN	DIMENSION TABLE	QTY
38	W=75mm, H=75mm, T=1.2mm & L=3000mm	70
39	W=100mm, H=75mm, T=1.2mm & L=3000mm	34

DRAWN BY	SHAH ALAM	
CHECKED BY	AMIR KHAN	
APPROVED BY	NASSER ANANI	
DATE	04/05/2026	
REF NO. :		
CONSULTANT :		

TITLE: CABLE TRUNKING W/COVER

CLIENT: SITE TECHNOLOGY INTEGRATED SYSTEM LLC

BONN METAL CONS. IND.

BONN GROUP OF COMPANIES
Cable Management Systems

SEC ITEM NO:


DWRG. NO. :


SHEET NO. :

SCALE: NTS

REV. 01

NOTE:-MATERIAL FINISH GI

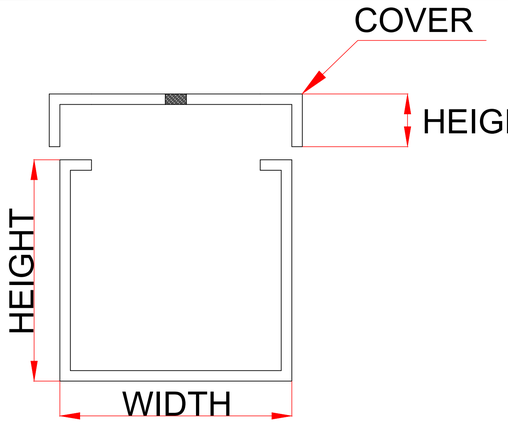

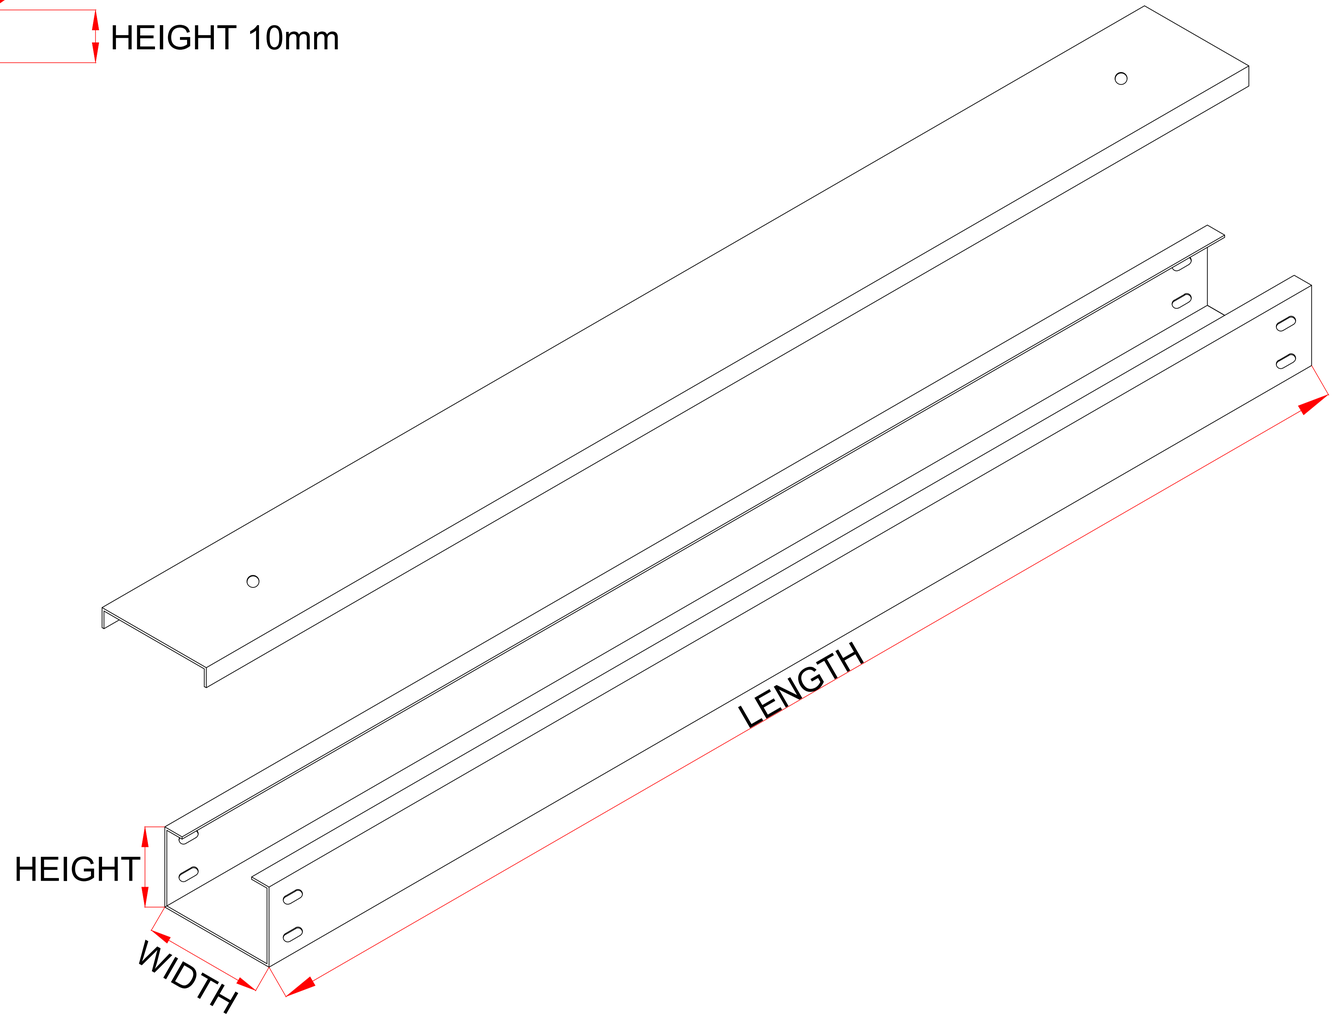

CABLE TRUNKING W/COVER

SN	DIMENSION TABLE	QTY
40	W=150mm, H=150mm, T=1.2mm & L=3000mm	29

DRAWN BY	SHAH ALAM	
CHECKED BY	AMIR KHAN	
APPROVED BY	NASSER ANANI	
DATE	04/05/2026	
REF NO. :		
CONSULTANT :		

TITLE: CABLE TRUNKING W/COVER

CLIENT: SITE TECHNOLOGY INTEGRATED SYSTEM LLC

BONN METAL CONS. IND.

MEBAR

BONN GROUP OF COMPANIES

Cable Management Systems

SEC ITEM NO:


DWRG. NO. :

SHEET NO. :

SCALE: NTS

REV. 01

NOTE:-MATERIAL FINISH GI

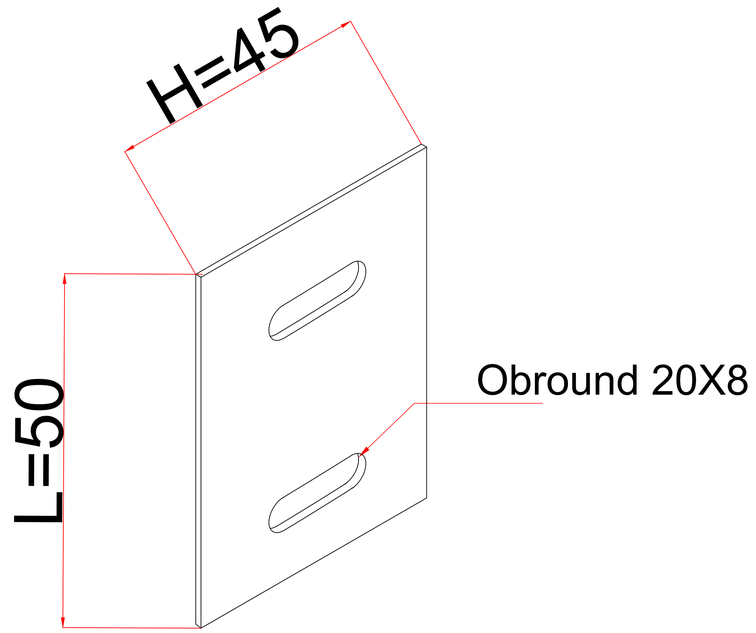

CABLE TRUNKING COUPLER

SN	DIMENSION TABLE	QTY
41	H=50mm, T=1.2mm	200

DRAWN BY	SHAH ALAM	
CHECKED BY	AMIR KHAN	
APPROVED BY	NASSER ANANI	
DATE	04/05/2026	
REF NO. :		
CONSULTANT :		

TITLE: CABLE TRUNKING COUPLER

CLIENT: SITE TECHNOLOGY INTEGRATED SYSTEM LLC

BONN METAL CONS. IND.

BONN GROUP OF COMPANIES
Cable Management Systems

SEC ITEM NO:


DWRG. NO. :

SHEET NO. :

SCALE: NTS

REV. 01

NOTE:-MATERIAL FINISH GI

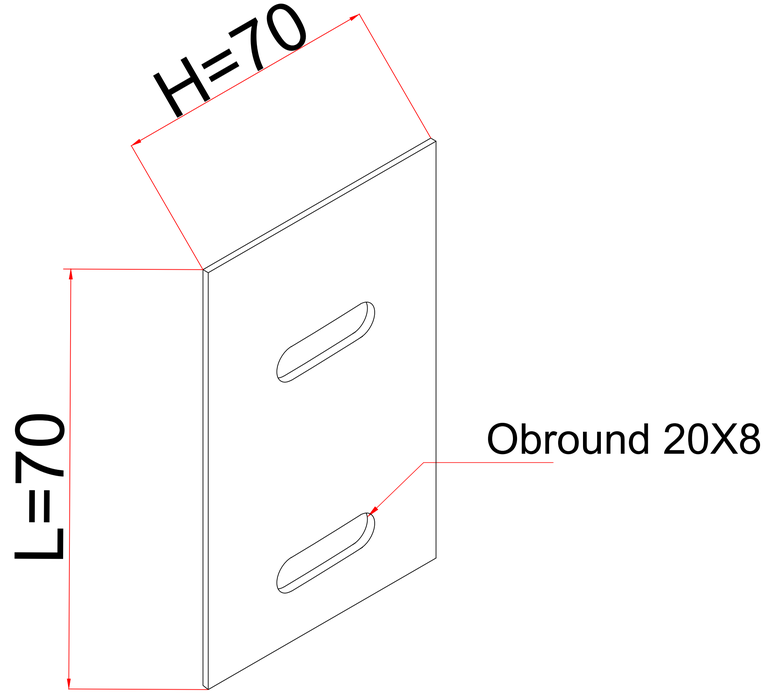

CABLE TRUNKING COUPLER

SN	DIMENSION TABLE	QTY	DRAWN BY	SHAH ALAM	
42	H=75mm, T=1.2mm	100	CHECKED BY	AMIR KHAN	
43	H=75mm, T=1.2mm	30	APPROVED BY	NASSER ANANI	
			DATE	04/05/2026	
			REF NO. :		
			CONSULTANT :		

TITLE: CABLE TRUNKING COUPLER

CLIENT: SITE TECHNOLOGY INTEGRATED SYSTEM LLC

BONN METAL CONS. IND.

METAR

BONN GROUP OF COMPANIES

Cable Management Systems

SEC ITEM NO:


DWRG. NO. :

SHEET NO. :

SCALE: NTS

REV. 01

NOTE:-MATERIAL FINISH GI

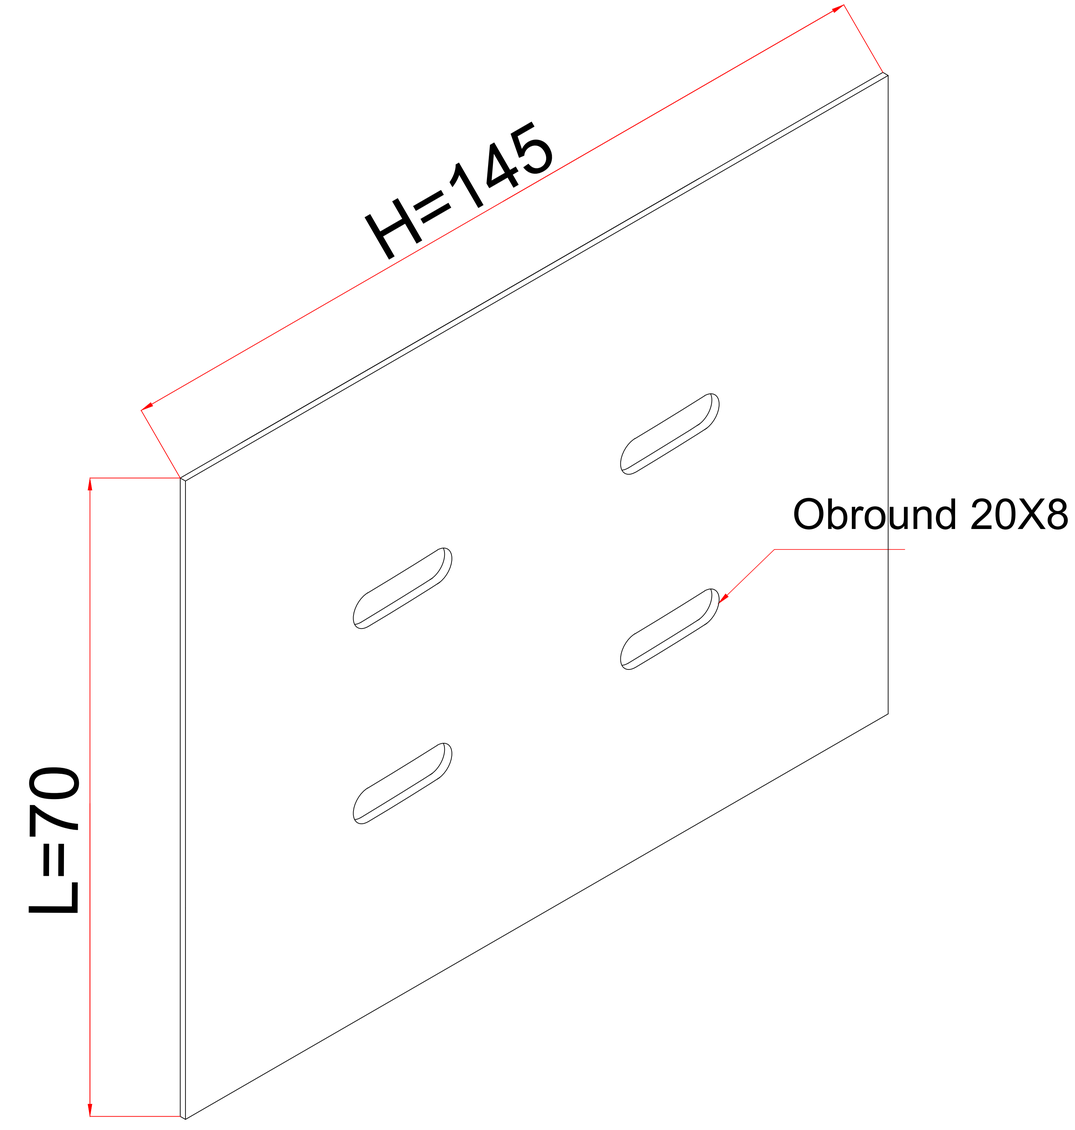

CABLE TRUNKING COUPLER

SN	DIMENSION TABLE	QTY
44	H=150mm, T=1.2mm	20

DRAWN BY	SHAH ALAM	
CHECKED BY	AMIR KHAN	
APPROVED BY	NASSER ANANI	
DATE	04/05/2026	
REF NO. :		
CONSULTANT :		

TITLE: CABLE TRUNKING COUPLER

CLIENT: SITE TECHNOLOGY INTEGRATED SYSTEM LLC

SEC ITEM NO:

BONN METAL CONS. IND.

METAR

BONN GROUP OF COMPANIES

Cable Management Systems


DWRG. NO. :

SHEET NO. :

SCALE: NTS

REV. 01

NOTE:-MATERIAL FINISH GI

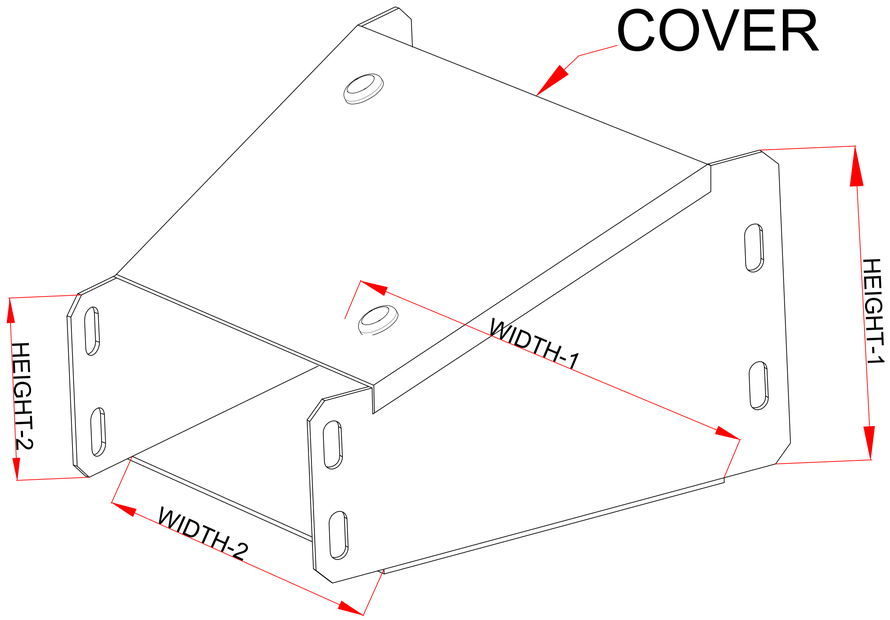

CABLE TRUNKING REDUCER W/COVER

SN	DIMENSION TABLE	QTY
45	W1=150mm,W2=100mm, H=100mm,T=1.2mm	20

DRAWN BY	SHAH ALAM	
CHECKED BY	AMIR KHAN	
APPROVED BY	NASSER ANANI	
DATE	04/05/2026	
REF NO. :		
CONSULTANT :		

TITLE: CABLE TRUNKING REDUCER W/COVER

CLIENT: SITE TECHNOLOGY INTEGRATED SYSTEM LLC

SEC ITEM NO:

BONN METAL CONS. IND.

BONN GROUP OF COMPANIES

Cable Management Systems


DWRG. NO. :

SHEET NO. :

SCALE: NTS

REV. 01

NOTE:-MATERIAL FINISH GI

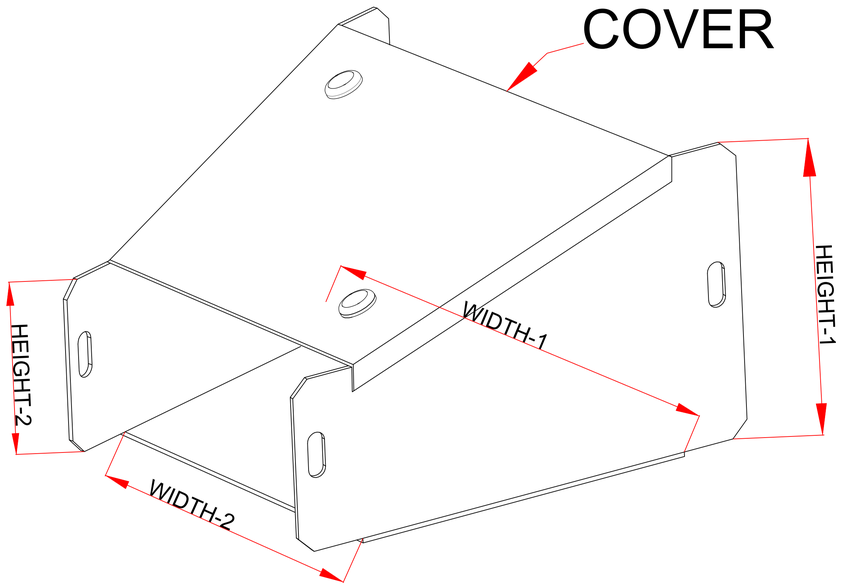


CABLE TRUNKING REDUCER W/COVER

SN	DIMENSION TABLE	QTY	DRAWN BY	SHAH ALAM		TITLE: CABLE TRUNKING REDUCER W/COVER	BONN METAL CONS. IND.		
46	W1=150mm,W2=75mm, H=75mm, T=1.2mm	20	CHECKED BY	AMIR KHAN					
			APPROVED BY	NASSER ANANI		CLIENT: SITE TECHNOLOGY INTEGRATED SYSTEM LLC			
			DATE	04/05/2026					
			REF NO. :			SEC ITEM NO:	DWRG. NO. :		REV.
			CONSULTANT :				SHEET NO. :	SCALE: NTS	01

METAR
BONN GROUP OF COMPANIES
Cable Management Systems

NOTE:-MATERIAL FINISH GI

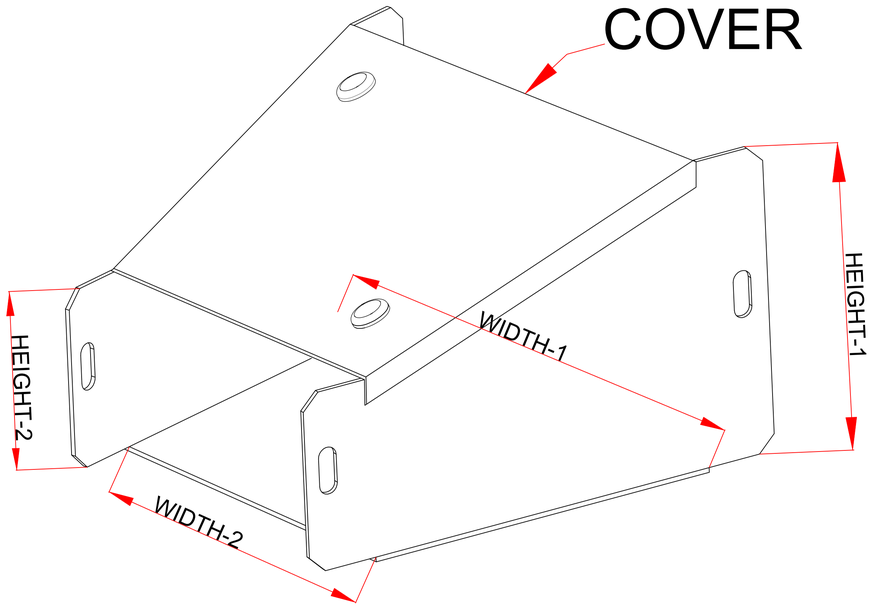

CABLE TRUNKING REDUCER W/COVER

SN	DIMENSION TABLE	QTY
47	W1=75mm,W2=50mm, H=50mm, T=1.2mm	50

DRAWN BY	SHAH ALAM	
CHECKED BY	AMIR KHAN	
APPROVED BY	NASSER ANANI	
DATE	04/05/2026	
REF NO. :		
CONSULTANT :		

TITLE: CABLE TRUNKING REDUCER W/COVER

CLIENT: SITE TECHNOLOGY INTEGRATED SYSTEM LLC

SEC ITEM NO:

BONN METAL CONS. IND.

BONN GROUP OF COMPANIES
Cable Management Systems


DWRG. NO. :

SHEET NO. :

SCALE: NTS

REV. 01

NOTE:-MATERIAL FINISH GI

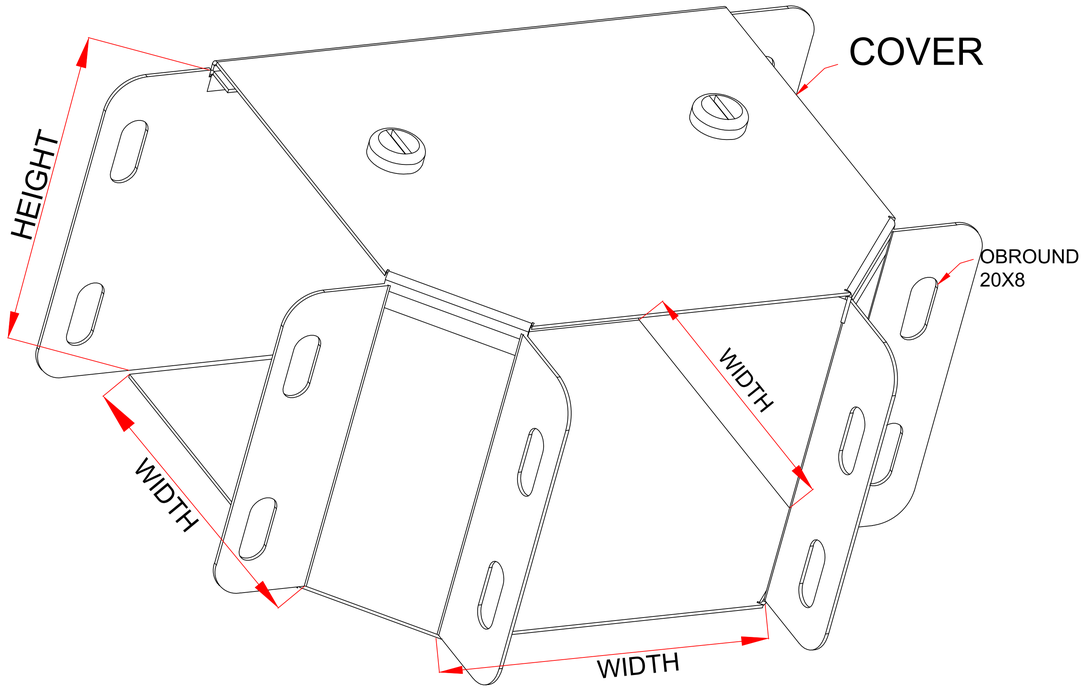

CABLE TRUNKING EQUAL TEE W/COVER

SN	DIMENSION TABLE	QTY
51	W=100mm, H=100mm, T=1.2mm	20

DRAWN BY	SHAH ALAM	
CHECKED BY	AMIR KHAN	
APPROVED BY	NASSER ANANI	
DATE	04/05/2026	
REF NO. :		
CONSULTANT :		

TITLE: CABLE TRUNKING EQUAL TEE W/COVER

CLIENT: SITE TECHNOLOGY INTEGRATED SYSTEM LLC

SEC ITEM NO:

BONN METAL CONS. IND.

METAR

BONN GROUP OF COMPANIES

Cable Management Systems


DWRG. NO. :

SHEET NO. :

SCALE: NTS

REV. 00

NOTE:-MATERIAL FINISH GI

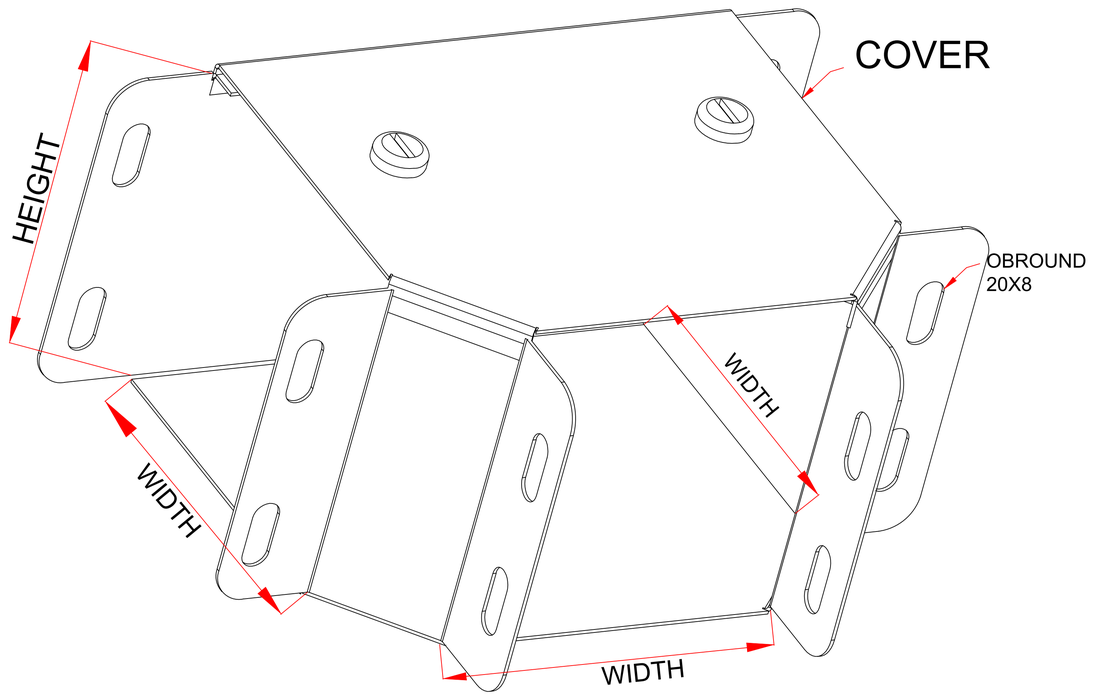

CABLE TRUNKING EQUAL TEE W/COVER

SN	DIMENSION TABLE	QTY
52	W=150mm, H=150mm, T=1.2mm	20

DRAWN BY	SHAH ALAM	
CHECKED BY	AMIR KHAN	
APPROVED BY	NASSER ANANI	
DATE	04/05/2026	
REF NO. :		
CONSULTANT :		

TITLE: CABLE TRUNKING EQUAL TEE W/COVER

CLIENT: SITE TECHNOLOGY INTEGRATED SYSTEM LLC

SEC ITEM NO:

BONN METAL CONS. IND.

BONN GROUP OF COMPANIES

Cable Management Systems


DWRG. NO. :

SHEET NO. :

SCALE: NTS

REV. 00

NOTE:-MATERIAL FINISH GI

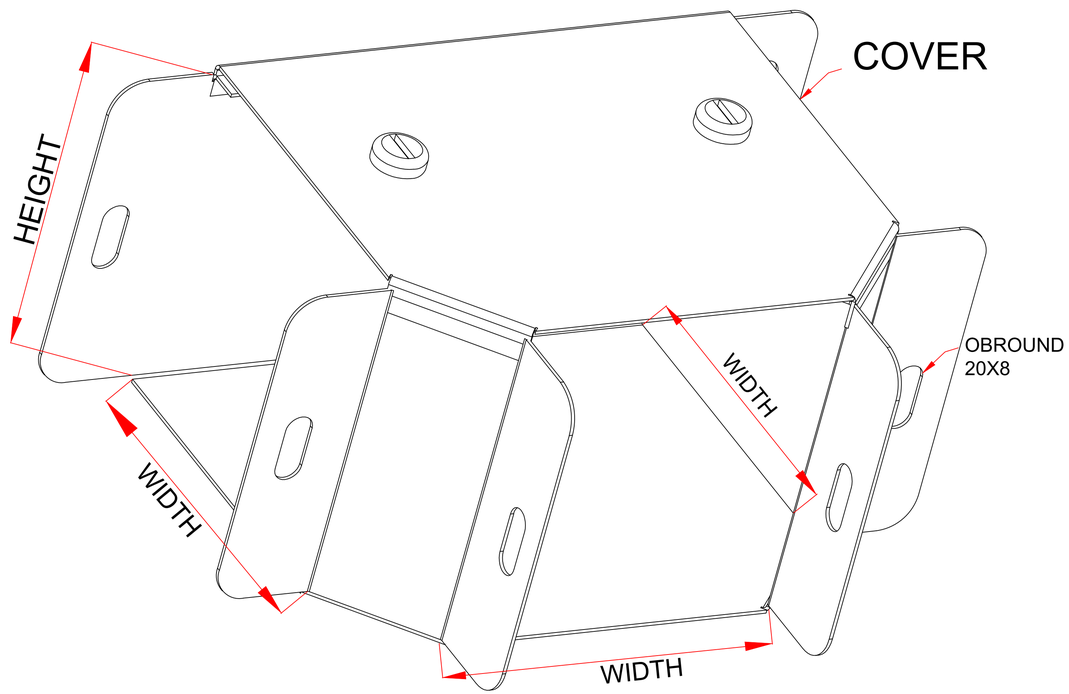

CABLE TRUNKING EQUAL TEE W/COVER

SN	DIMENSION TABLE	QTY
53	W=75mm, H=75mm, T=1.2mm	40

DRAWN BY	SHAH ALAM	
CHECKED BY	AMIR KHAN	
APPROVED BY	NASSER ANANI	
DATE	04/05/2026	
REF NO. :		
CONSULTANT :		

TITLE: CABLE TRUNKING EQUAL TEE W/COVER

CLIENT: SITE TECHNOLOGY INTEGRATED SYSTEM LLC

SEC ITEM NO:

BONN METAL CONS. IND.

METAR

BONN GROUP OF COMPANIES

Cable Management Systems


DWRG. NO. :

SHEET NO. :

SCALE: NTS

REV. 00

NOTE:-MATERIAL FINISH GI

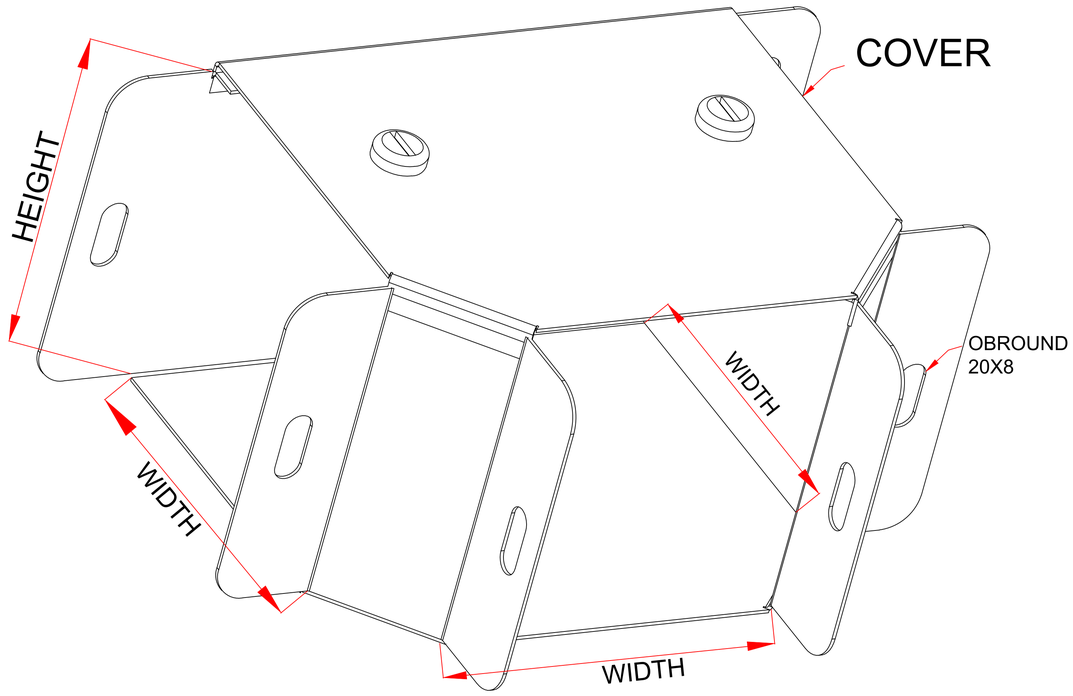

CABLE TRUNKING EQUAL TEE W/COVER

SN	DIMENSION TABLE	QTY
54	W=50mm, H=50mm, T=1.2mm	50

DRAWN BY	SHAH ALAM	
CHECKED BY	AMIR KHAN	
APPROVED BY	NASSER ANANI	
DATE	04/05/2026	
REF NO. :		
CONSULTANT :		

TITLE: CABLE TRUNKING EQUAL TEE W/COVER

CLIENT: SITE TECHNOLOGY INTEGRATED SYSTEM LLC

SEC ITEM NO:

BONN METAL CONS. IND.

BONN GROUP OF COMPANIES

Cable Management Systems


DWRG. NO. :

SHEET NO. :

SCALE: NTS

REV. 00

NOTE:-MATERIAL FINISH GI

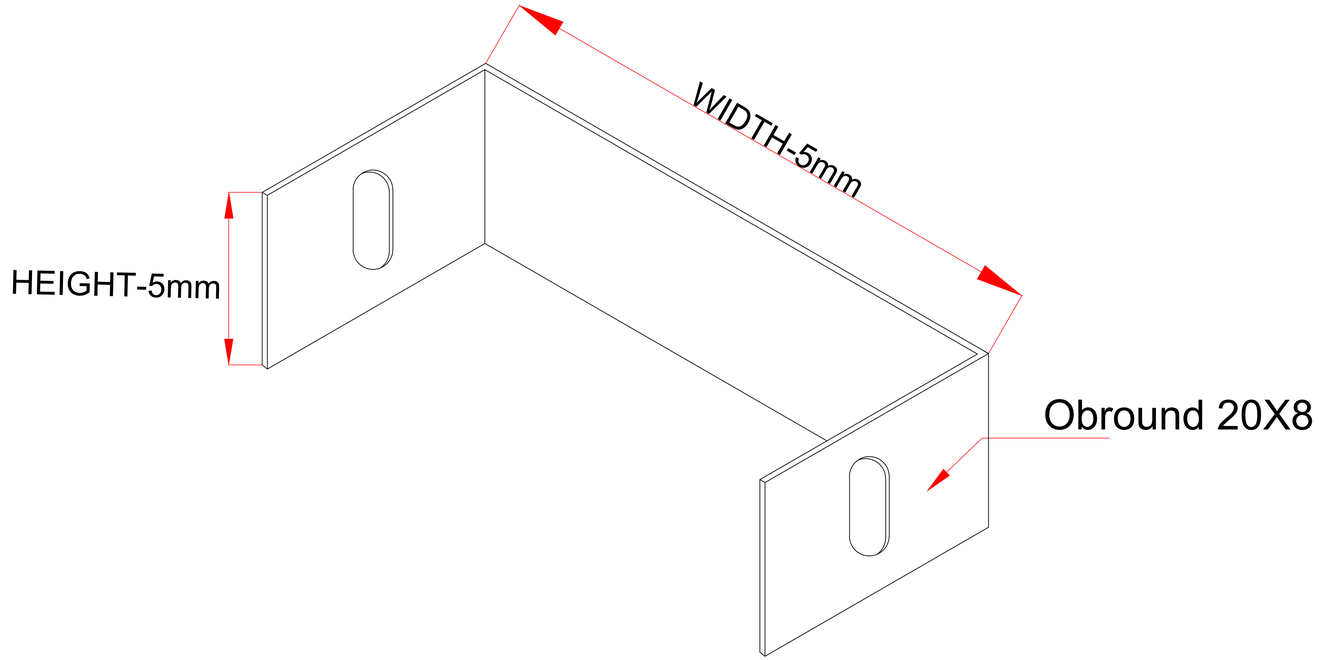

CABLE TRUNKING END CAP

SN	DIMENSION TABLE	QTY
59	W=50mm, H=50mm, T=1.2mm	04

DRAWN BY	SHAH ALAM	
CHECKED BY	AMIR KHAN	
APPROVED BY	NASSER ANANI	
DATE	04/05/2026	
REF NO. :		
CONSULTANT :		

TITLE: CABLE TRUNKING END CAP

CLIENT: SITE TECHNOLOGY INTEGRATED SYSTEM LLC

SEC ITEM NO:

BONN METAL CONS. IND.

METAR

BONN GROUP OF COMPANIES

Cable Management Systems


DWRG. NO. :

SHEET NO. :

SCALE: NTS

REV. 01

NOTE:-MATERIAL FINISH GI

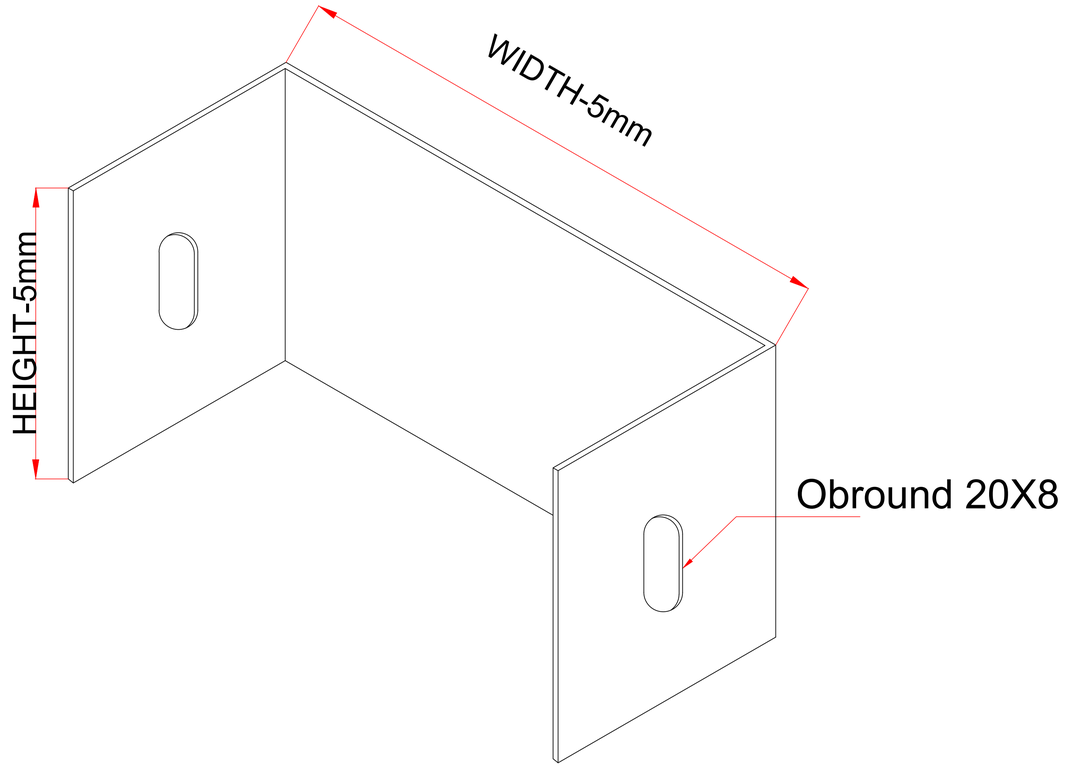

CABLE TRUNKING END CAP

SN	DIMENSION TABLE	QTY
60	W=75mm, H=75mm, T=1.2mm	04
62	W=100mm, H=75mm, T=1.2mm	10

DRAWN BY	SHAH ALAM	
CHECKED BY	AMIR KHAN	
APPROVED BY	NASSER ANANI	
DATE	04/05/2026	
REF NO. :		
CONSULTANT :		

TITLE: CABLE TRUNKING END CAP

CLIENT:SITE TECHNOLOGY INTEGRATED SYSTEM LLC

SEC ITEM NO:

BONN METAL CONS. IND.

BONN GROUP OF COMPANIES
Cable Management Systems


DWRG. NO. :

SHEET NO. :

SCALE: NTS

REV. 01

NOTE:-MATERIAL FINISH GI

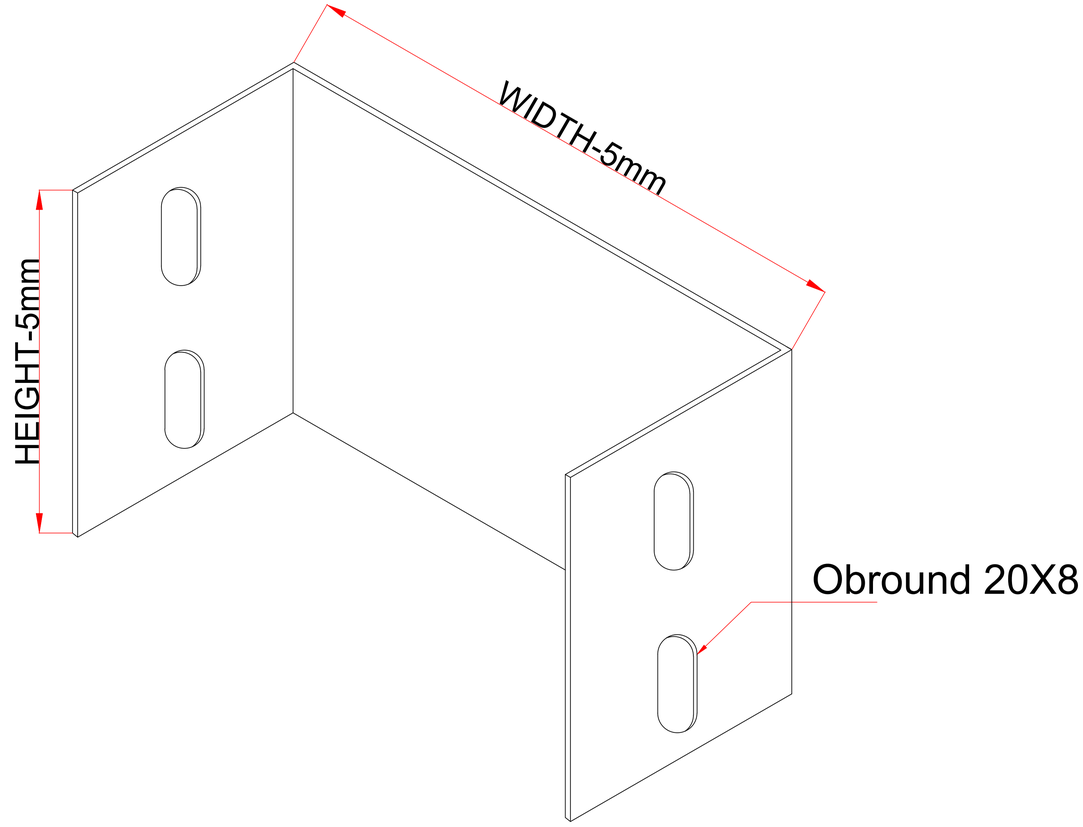

CABLE TRUNKING END CAP

SN	DIMENSION TABLE	QTY
61	W=150mm, H=150mm, T=1.2mm	15

DRAWN BY	SHAH ALAM	
CHECKED BY	AMIR KHAN	
APPROVED BY	NASSER ANANI	
DATE	04/05/2026	
REF NO. :		
CONSULTANT :		

TITLE: CABLE TRUNKING END CAP

CLIENT: SITE TECHNOLOGY INTEGRATED SYSTEM LLC

BONN METAL CONS. IND.

METAIR

BONN GROUP OF COMPANIES

Cable Management Systems

SEC ITEM NO:


DWRG. NO. :

SHEET NO. :


SCALE: NTS

REV. 01


NOTE:- MATERIAL FINISH GI

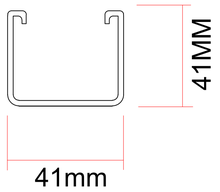

FRONT VIEW

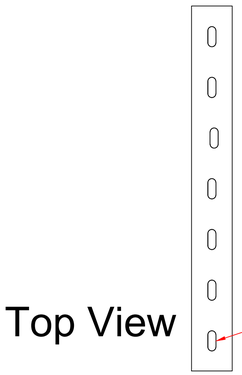

Top View

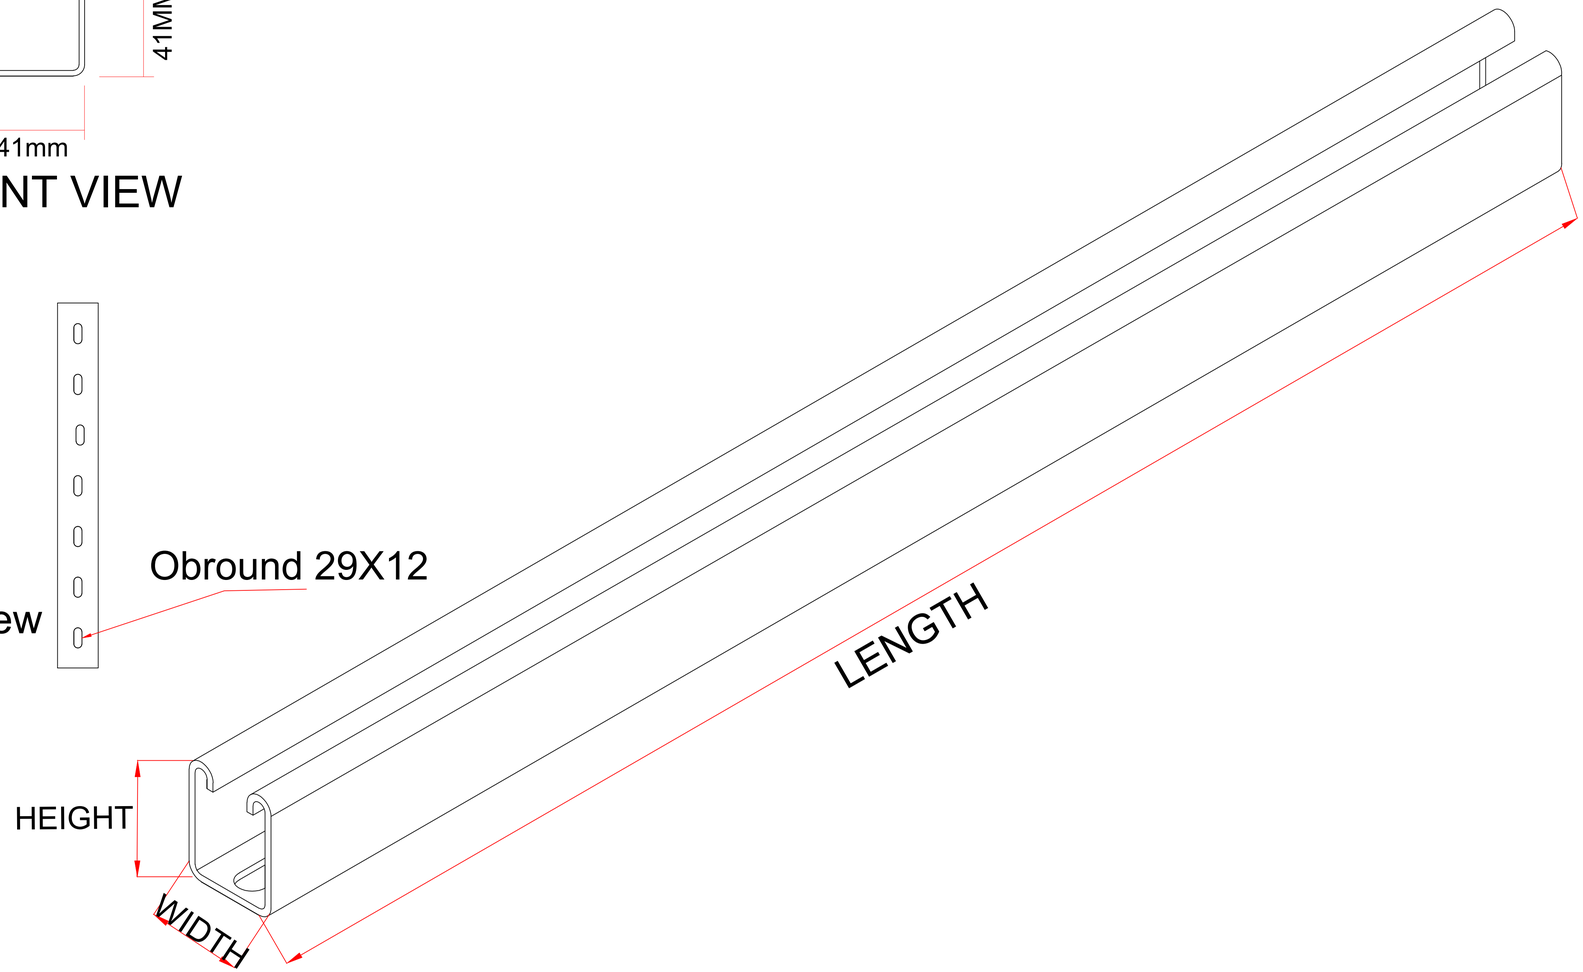

UNISTRUT SLOTTED CHANNEL

SN.30	DIMENSION TABLE	QTY
70	W=41mm, H=41mm, T=2.0mm & L=3000mm	250

DRAWN BY	SHAH ALAM	
CHECKED BY	AMIR KHAN	
APPROVED BY	NASSER ANANI	
DATE	04/05/2026	
REF NO. :		
CONSULTANT :		

TITLE: UNISTRUT SLOTTED CHANNEL

CLIENT: SITE TECHNOLOGY INTEGRATED SYSTEM LLC

SEC ITEM NO:

BONN METAL CONS. IND.

METAR

BONN GROUP OF COMPANIES

Cable Management Systems

DWRG. NO. :

SHEET NO. :

SCALE: NTS

REV. 01